


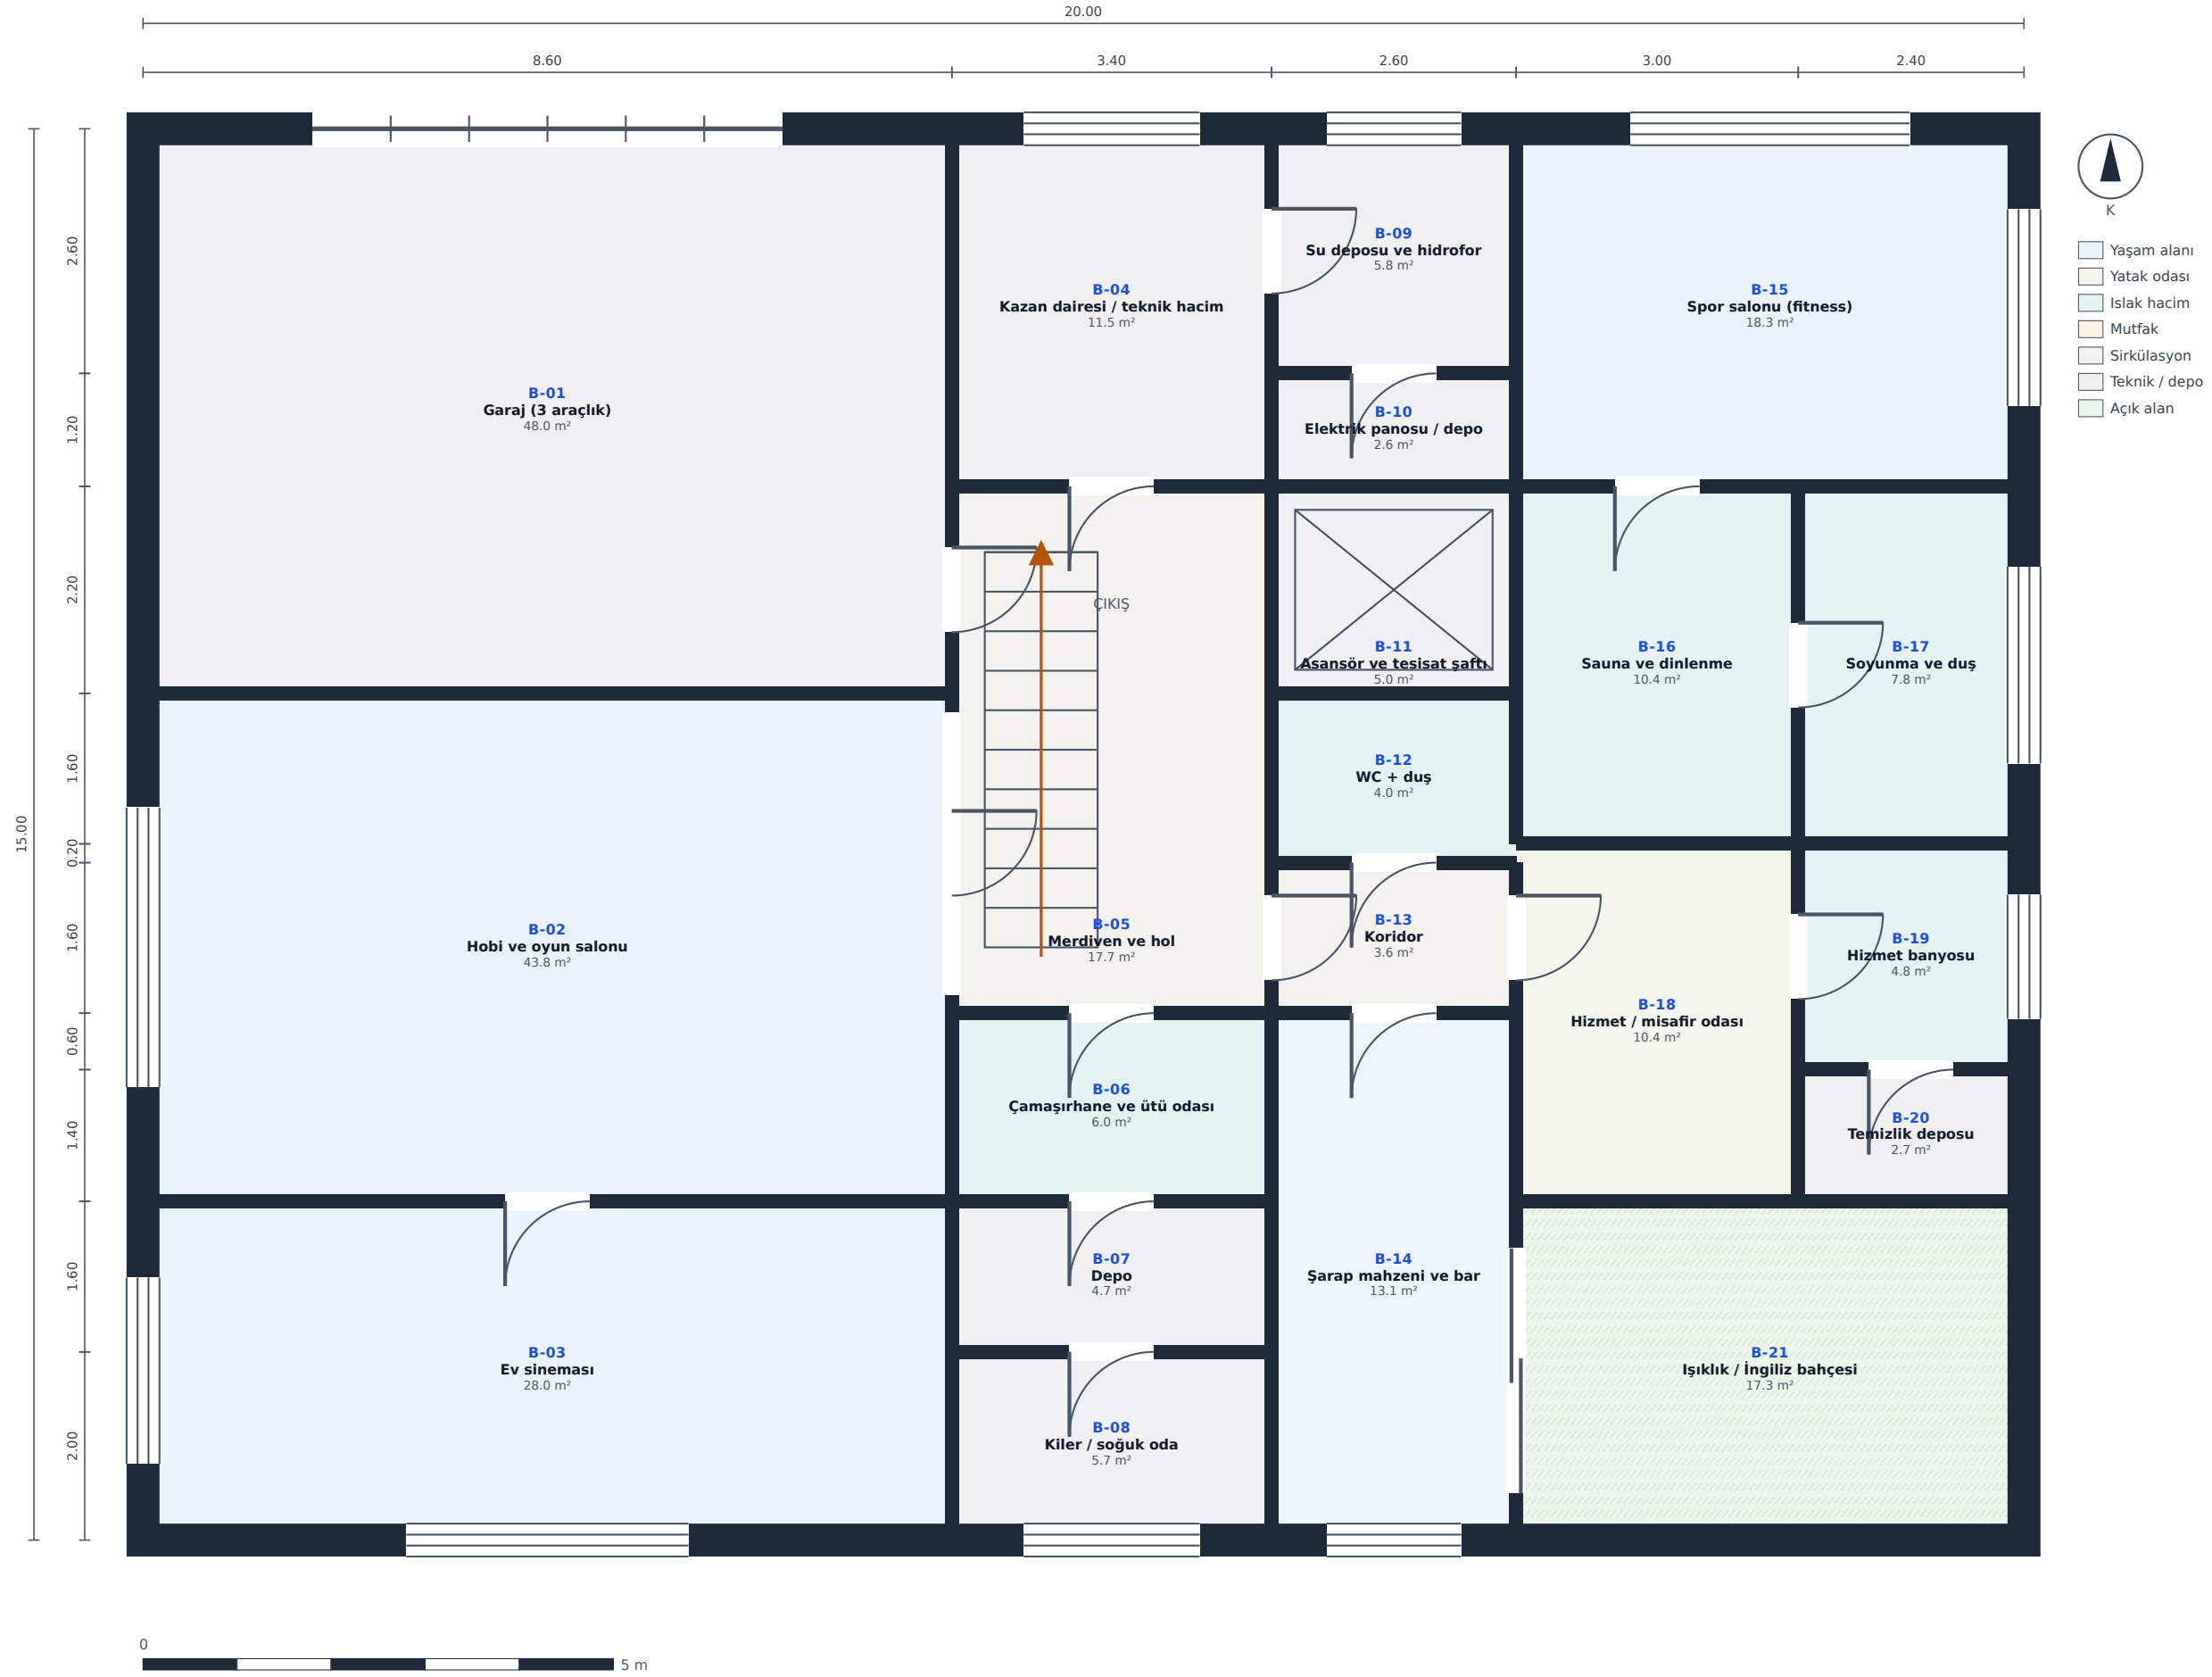

BODRUM PLANI


Net kapalı alan 253.9 m² · açık alan 17.3 m² · brüt kat alanı 300,0 m²

Kat yüksekliği 2.90 m · net tavan yüksekliği 2.55 m · duvarlar: dış 35 cm (19 tuğla + 8 XPS + kaplama), iç 15 cm

DURUNDAY VİLLA

Konya / Meram / Durunday — Bodrumlu dubleks villa

Ölçek 1:100 (A3) · Ön tasarım · 19.09.2026

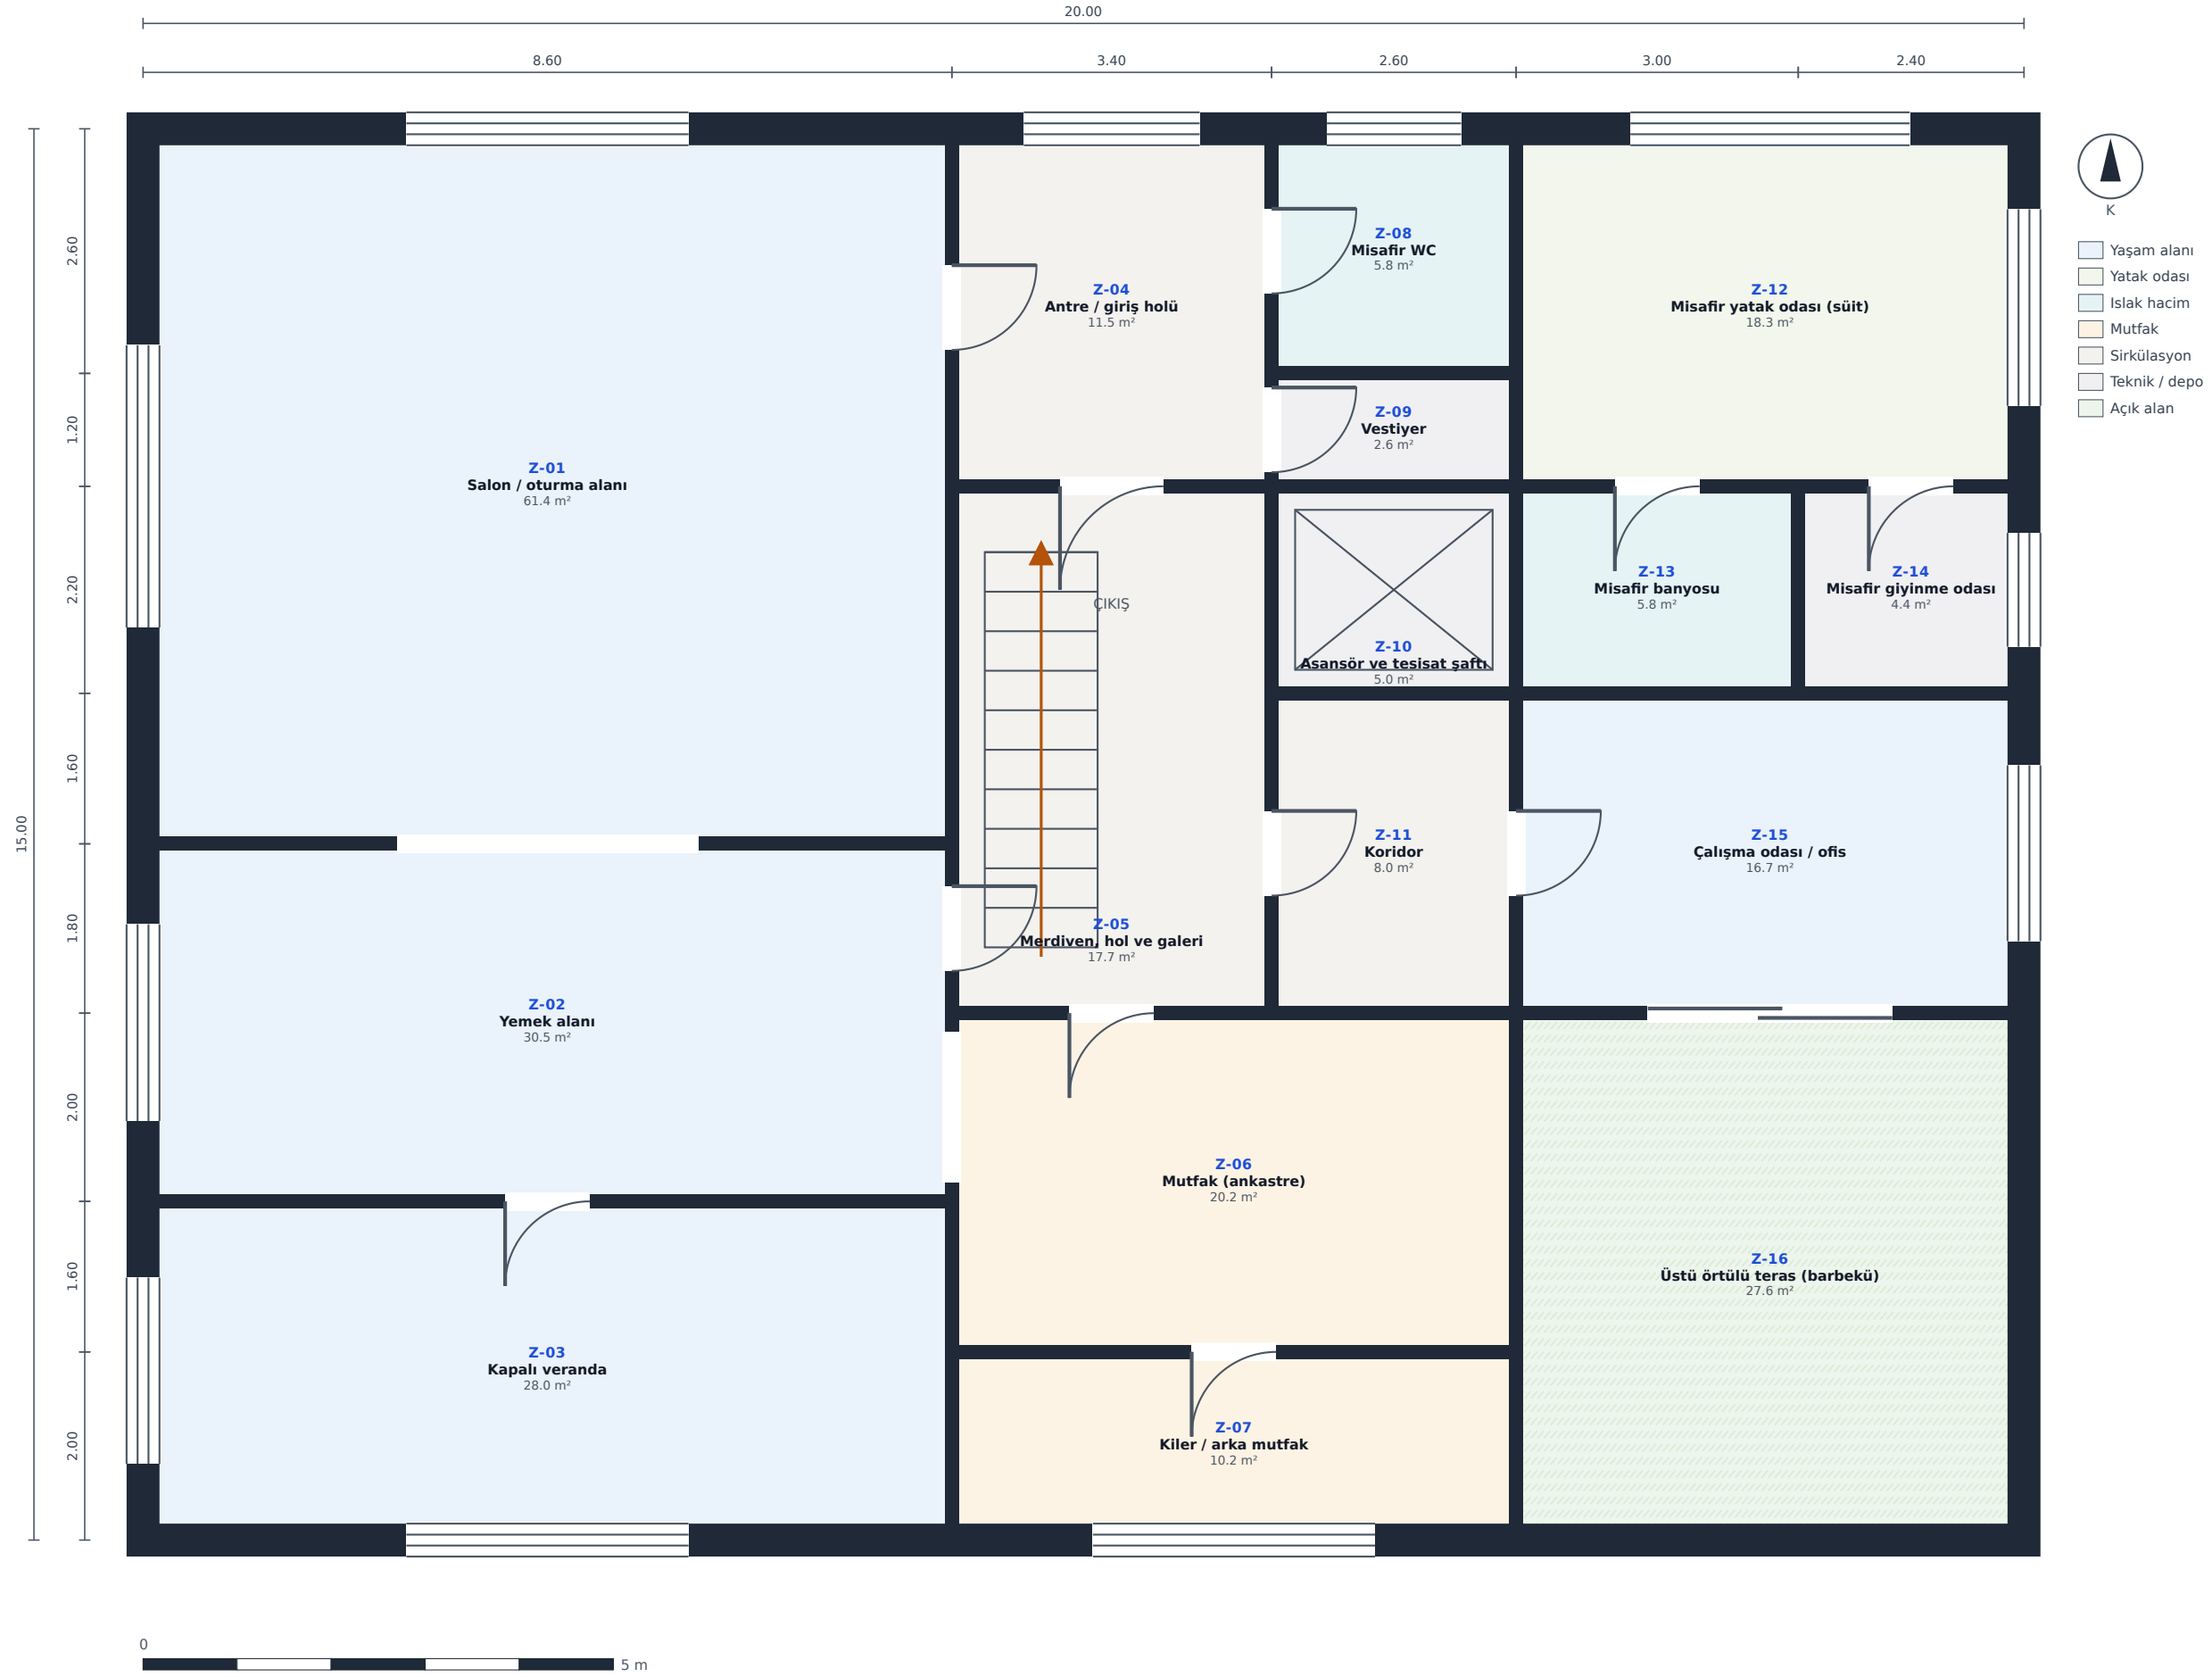

ZEMİN PLANI

Net kapalı alan 246.1 m² · açık alan 27.6 m² · brüt kat alanı 300,0 m²

Kat yüksekliği 3.20 m · net tavan yüksekliği 2.85 m · duvarlar: dış 35 cm (19 tuğla + 8 XPS + kaplama), iç 15 cm

DURUNDAY VİLLA

Konya / Meram / Durunday — Bodrumlu dubleks villa

Ölçek 1:100 (A3) · Ön tasarım · 19.09.2026



1. KAT PLANI


Net kapalı alan 247.5 m² · açık alan 23.6 m² · brüt kat alanı 300,0 m²

Kat yüksekliği 3.10 m · net tavan yüksekliği 2.75 m · duvarlar: dış 35 cm (19 tuğla + 8 XPS + kaplama), iç 15 cm

DURUNDAY VİLLA

Konya / Meram / Durunday — Bodrumlu dubleks villa

Ölçek 1:100 (A3) · Ön tasarım · 19.09.2026

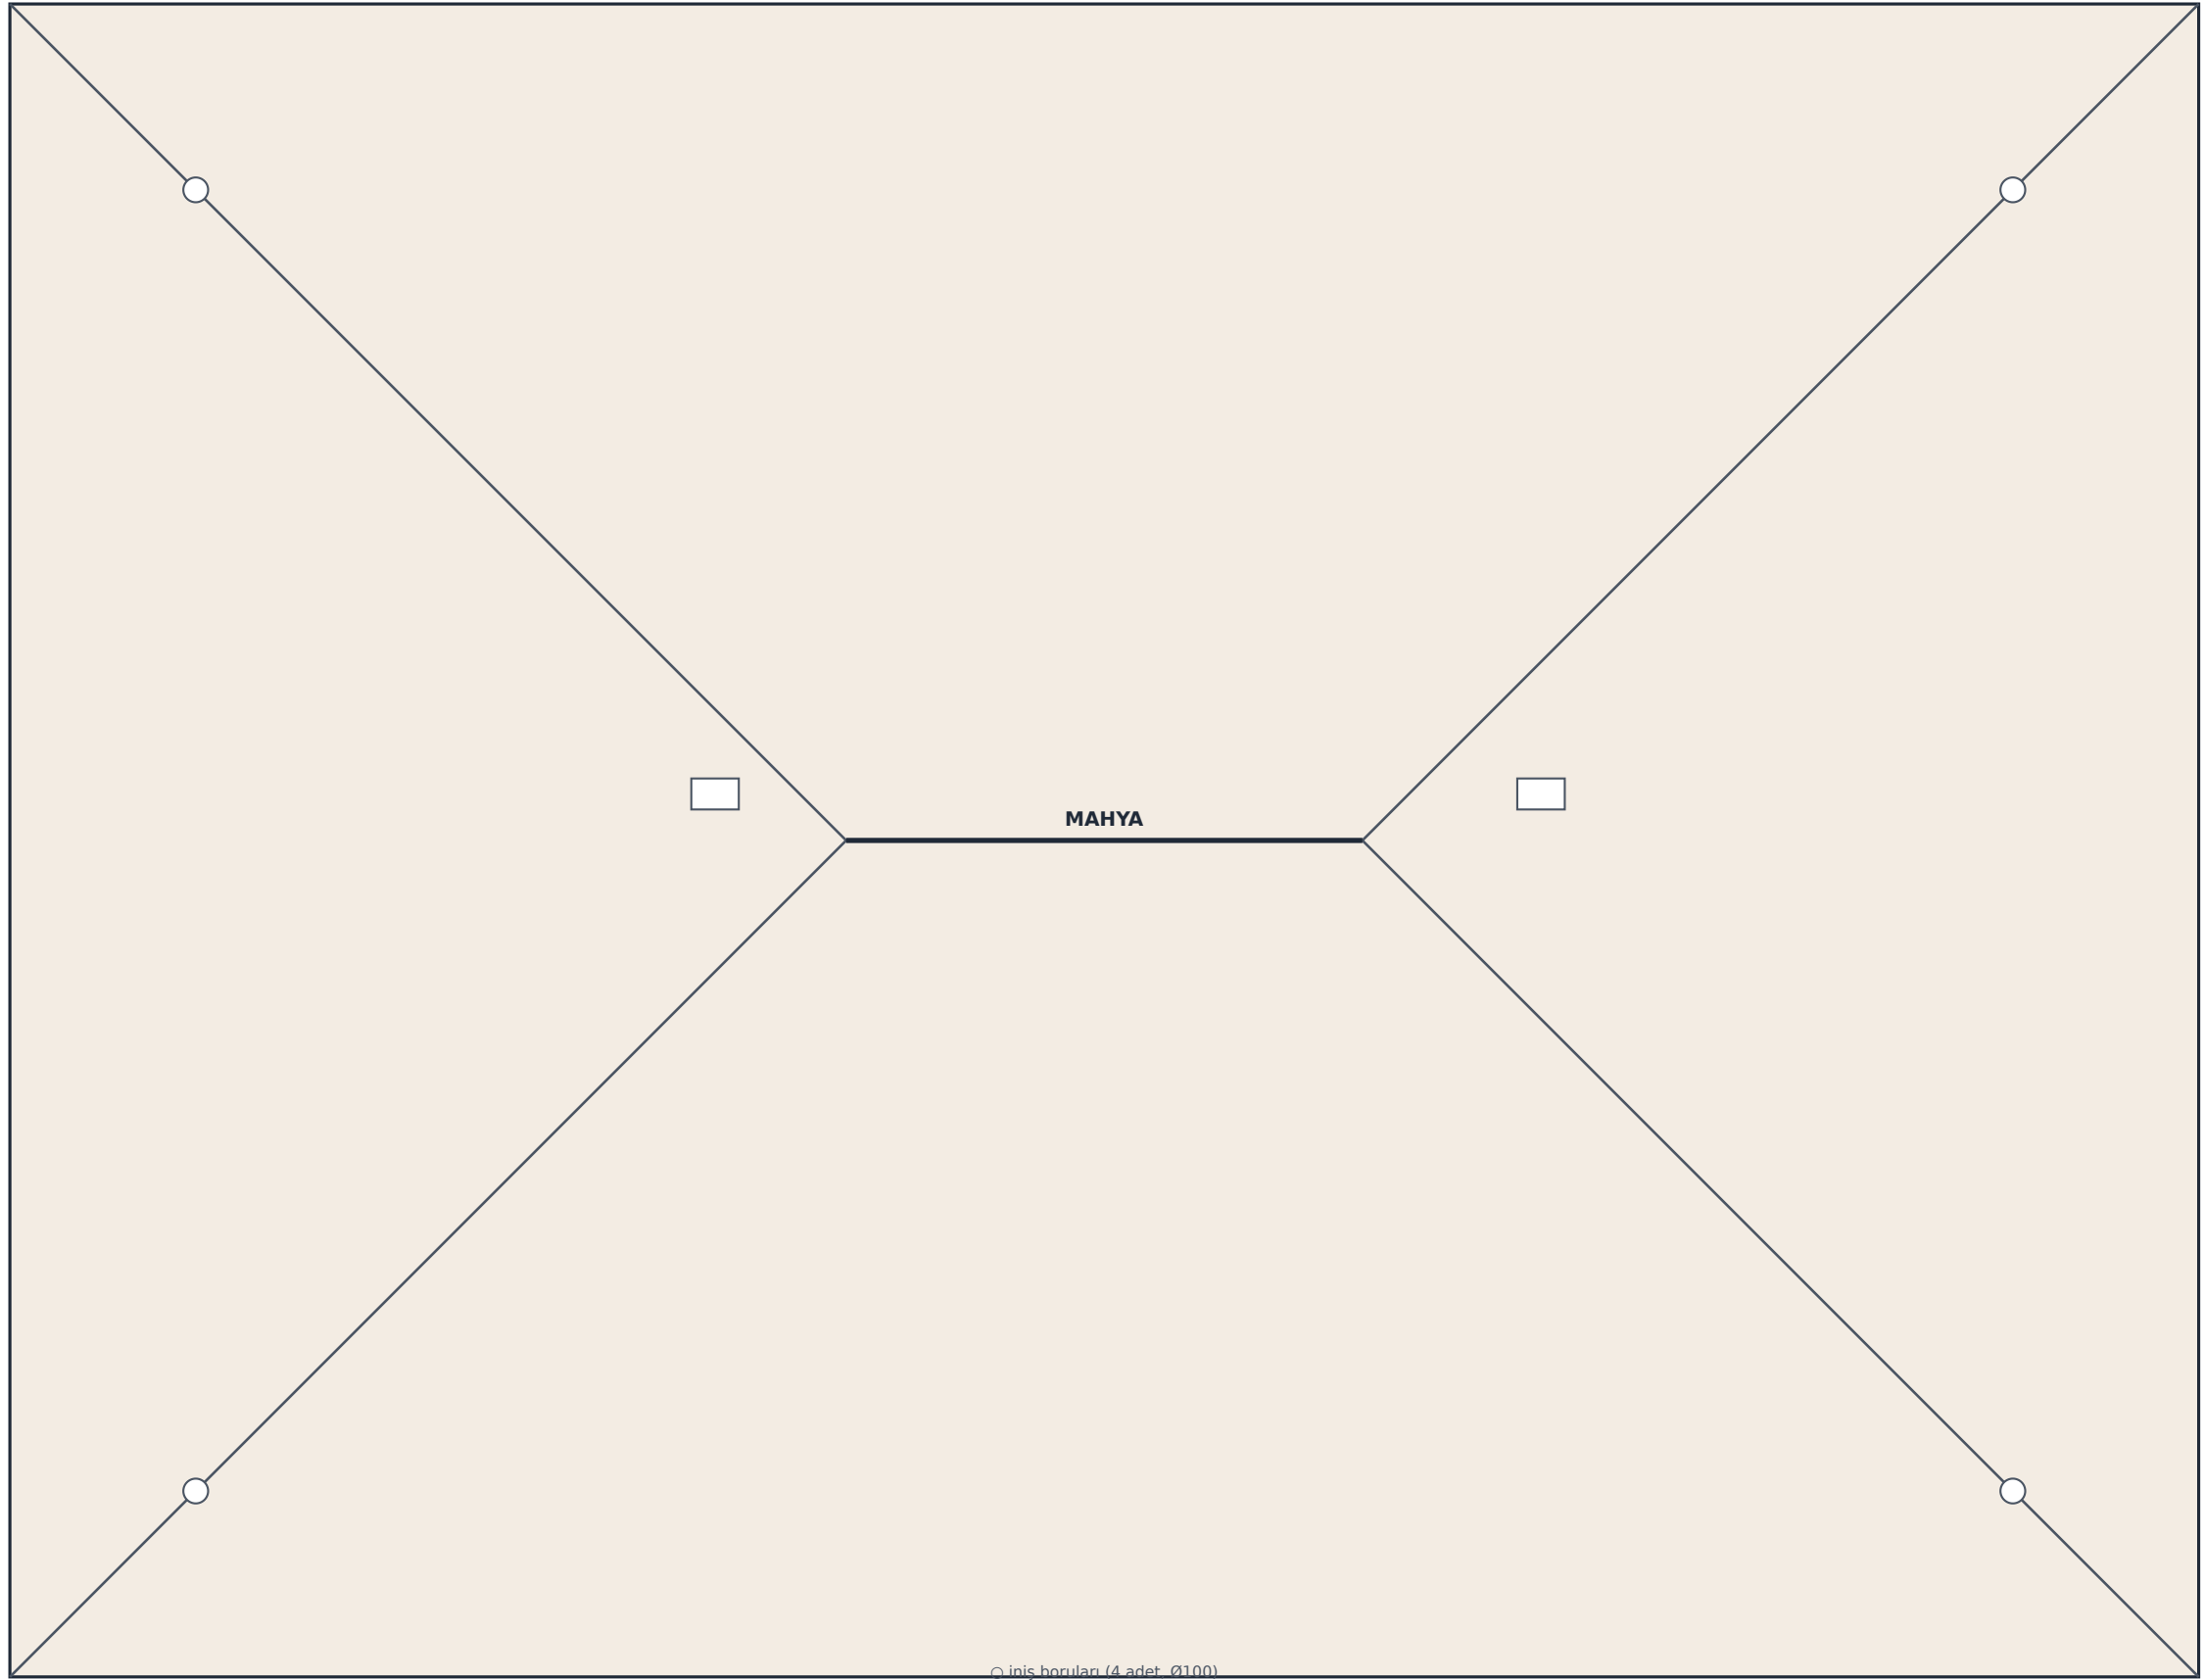

ÇATI PLANI


Kırma çatı · 4 yöne eğimli · mahya ve dere çizgileri · alüminyum oluk ve iniş boruları

Saçak taşması 60 cm · kilitli kiremit · çatı arası havalandırma menfezleri

DURUNDAY VİLLA

Konya / Meram / Durunday — Bodrumlu dubleks villa

Ölçek 1:100 (A3) · Ön tasarım · 19.09.2026

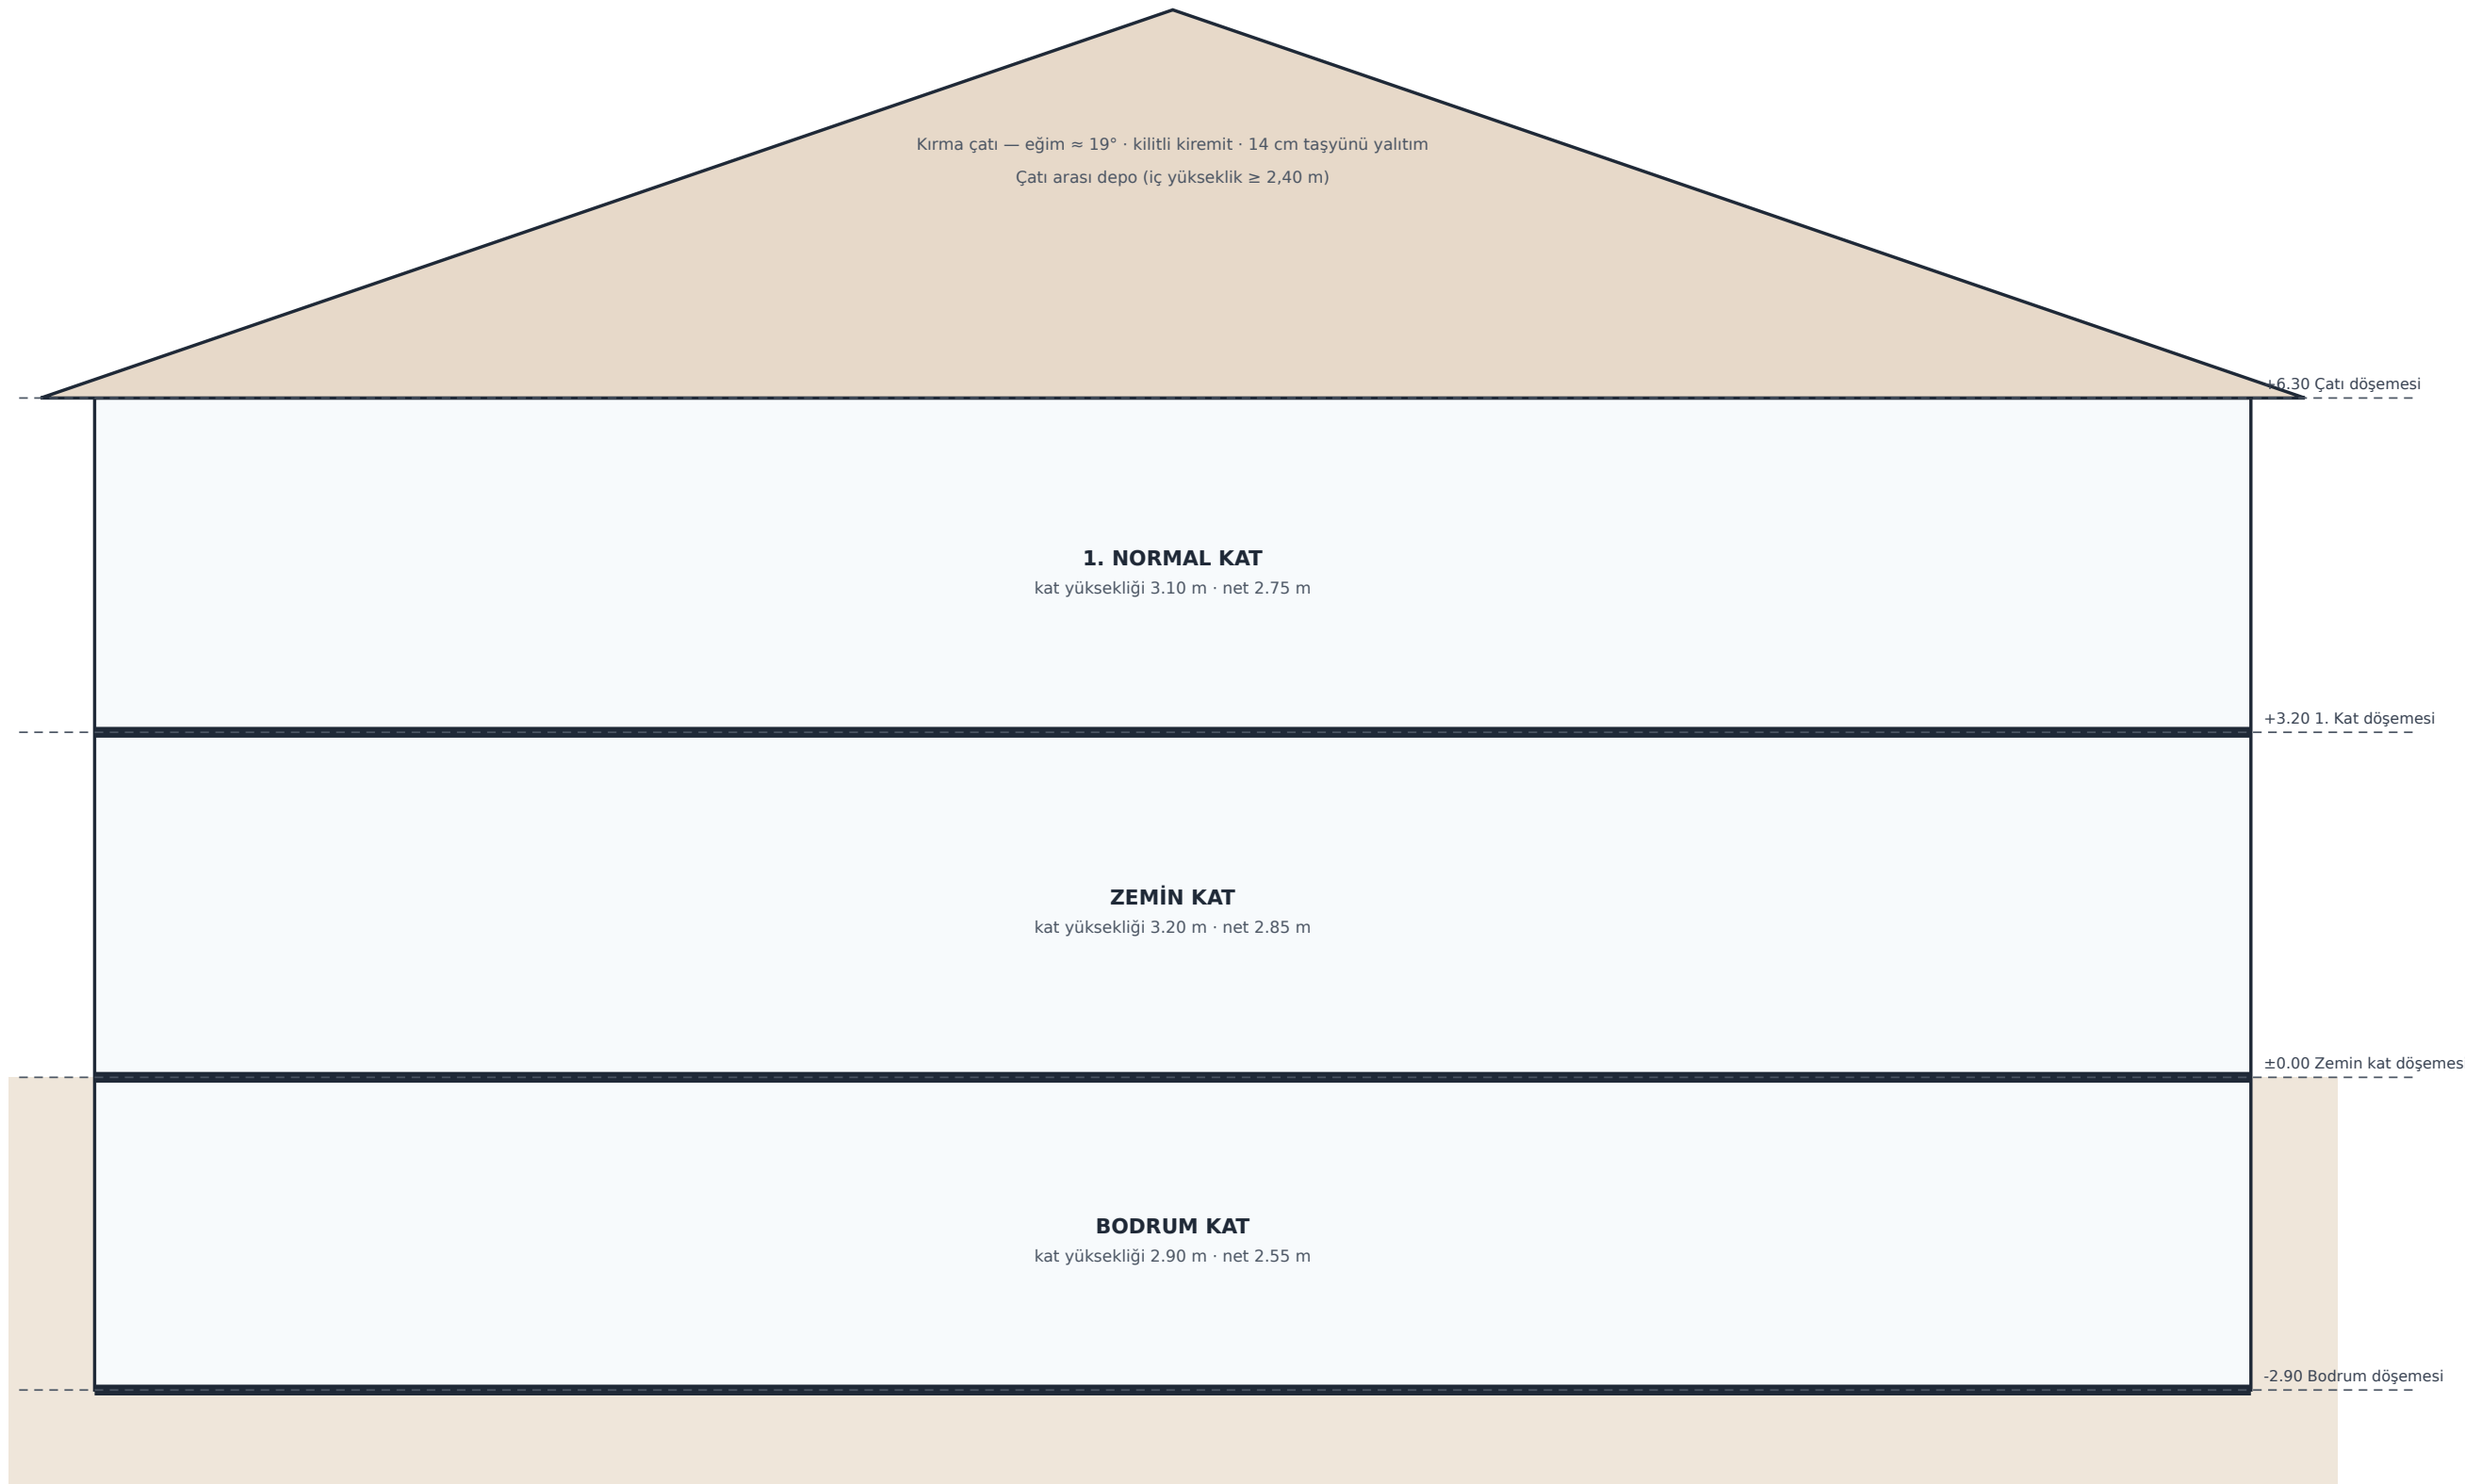

A-A KESİTİ

Bodrum 2.90 + Zemin 3.20 + 1. Kat 3.10 + kırma çatı — toplam yapı yüksekliği 12.80 m

Net tavan yüksekliği her katta $\geq 2,55$ m (yönetmelik asgarisi 2,40 m) · döşeme kalınlığı 30 cm

DURUNDAY VİLLA

Konya / Meram / Durunday — Bodrumlu dubleks villa

Ölçek 1:100 (A3) · Ön tasarım · 19.09.2026