



DURUNDAY VÄ°LLA

Konya Â· Meram Â· Durunday â€" bodrumlu dubleks mâ¼stakil konut

Mimari Â¶n proje (avan) Âşizim seti Â· Revizyon R1 Â· 21.09.2026

PAFTA LÄ°STESÄ°

A-00	KAPAK VE PAFTA LÄ°STESÄ°	â€"	A-07	BÄ°B KESÄ°TÄ°	1/100
A-01	VAZÄ°YET PLANI	1/200	A-08	KUZEY VE GÄ°NEY GÄ-RÄ°NÄ°ZLERÄ°	1/100
A-02	BODRUM KAT PLANI	1/100	A-09	DOÄŰU VE BATI GÄ-RÄ°NÄ°ZLERÄ°	1/100
A-03	ZEMÄ°N KAT PLANI	1/100	A-10	SÄ°STEM KESÄ°TÄ°	1/50
A-04	1. KAT PLANI	1/100	A-11	MERDÄ°VEN DETAYI	1/50
A-05	Ä°ATI PLANI	1/100	A-12	DOÄŰRAMA LÄ°STESÄ°	â€"
A-06	AÄ°A KESÄ°TÄ°	1/100			

ALAN Ä-ZETÄ°

Kat	BrÄ¼t	Net
Bodrum	300,00	242,60
Zemin	300,00	246,30
1. Kat	300,00	236,90
Toplam	900,00	725,80

Parsel 1.001 mâ² Â· TAKS 0,30 Â· KAKS 0,60
Emsal alanÄ± 600 mâ² (zemin + 1. kat)
Teras 80 mâ² Â· balkon 19 mâ² Â· pergola 30 mâ²
Otopark: 2 kapalı + 2 açık

DURUNDAY VÄ°LLA

Konya Â· Meram Â· Durunday

Bodrumlu dubleks mâ¼stakil konut Â· 300 mâ² oturum

MÄ°MARÄ° Ä-N PROJE (AVAN)

Ruhsat ve uygulamaya esas deÄYildir

NOTLAR

- Bu set Â¶n tasarÄ±m (avan) niteliÄYindedir; ruhsata esas mimari, statik, mekanik ve elektrik projeleri yetkili mâ¼elliflerce hazırlanacaktır.
- Parsel, imar ve kot bilgileri varsayımdır; Meram Belediyesi imar durumu ve hâlihazır harita ile teyit edilmelidir.
- Ä-İÄŞÄ¼er cm, kotlar m'dir. Ä±0.00 = zemin kat bitimiÄ¼ dÄ¼Yemesi = tabii zemin +0.30.
- TÄ¼m patfalar tek veri kaynağından (veri.py) Ä¼retilir; plan, kesit, gÄ¼rÄ¼Ä¼ ve tablolar birbiriyle tutarlıdır.

REVÄ°ZYONLAR

R0	19.09.2026	Ä¼k yayÄ±n
R1	21.09.2026	Plan kurgusu yeniden dÄ¼zenlendi; kesit, gÄ¼rÄ¼Ä¼, detay ve doÄ¼rama listesi eklendi

Ä°Ä SAHÄ°BÄ° â€"	HAZIRLAYAN E. Ceran
MÄ°ELLÄ°F MÄ°MAR (ruhsat aÄYamasında atanacak)	Ä°MZA

PAFTA ADI

KAPAK VE PAFTA LÄ°STESÄ°

Ä-LÄ¼EK â€"	TARÄ¼H 21.09.2026	PAFTA NO A-00
----------------	----------------------	------------------

DURUNDAY VÄ°LLA

Konya Â· Meram Â· Durunday

Bodrumlu dubleks mâ°stakil konut Â· 300 mâ² oturum

MÂ°MARÂ° Â-N PROJE (AVAN)

Ruhsat ve uygulamaya esas deÄYildir

LEJANT

- Havuz
- Sert zemin / taÄY dÄ°ÄYeme
- 1 AÄYâÄ° (mevcut/dikilecek)

NOTLAR

- AraÄ° giriÄYi doÄYruda, garaja doÄYrudan (rampa yok); Ä°nÄ°nde 2 araÄ°lÄ±k aÄ°lÄ±k park yeri.
- Yaya giriÄYi ayrÄ± kapÄ±dan, giriÄY saÄ°pÄYÄ±na yÄ°Ä°Ä°ÄY yolu ile.
- Servis yolu doÄYr yan bahÄ°den arka mutfak kapÄ±sÄ±na ulaÄYÄ±.
- BahÄ° duvarÄ±: yol cephesinde 50 cm taÄY + 100 cm antrasit metal Ä°it; yan ve arka sÄ±nÄ±rlarda 180 cm.
- Havuz arka bahÄ°de; makine dairesi bodrumda (B-16).
- Selvi dizileri yan komÄYlara gÄ°rsel perde oluÄYturur.



REVÄ°ZYONLAR

R0	19.09.2026	Ä°lk yayÄ±n
R1	21.09.2026	Plan kurgusu yeniden dÄ°zenlendi; kesit, gÄ°rÄ°nÄ°ÄY, detay ve doÄYrama listesi eklendi

Ä°Ä° SAHÄ°BÄ°

â€™

HAZIRLAYAN

E. Ceran

MÂ°ELLÄ°F MÂ°MAR

(ruhsat aÄYamasÄ±nda atanacak)

Ä°MZA

PAFTAADI

VAZÄ°YET PLANI

Ä°LÄ±EK


1/200

TARÄ°H

21.09.2026

PAFTA NO

A-01

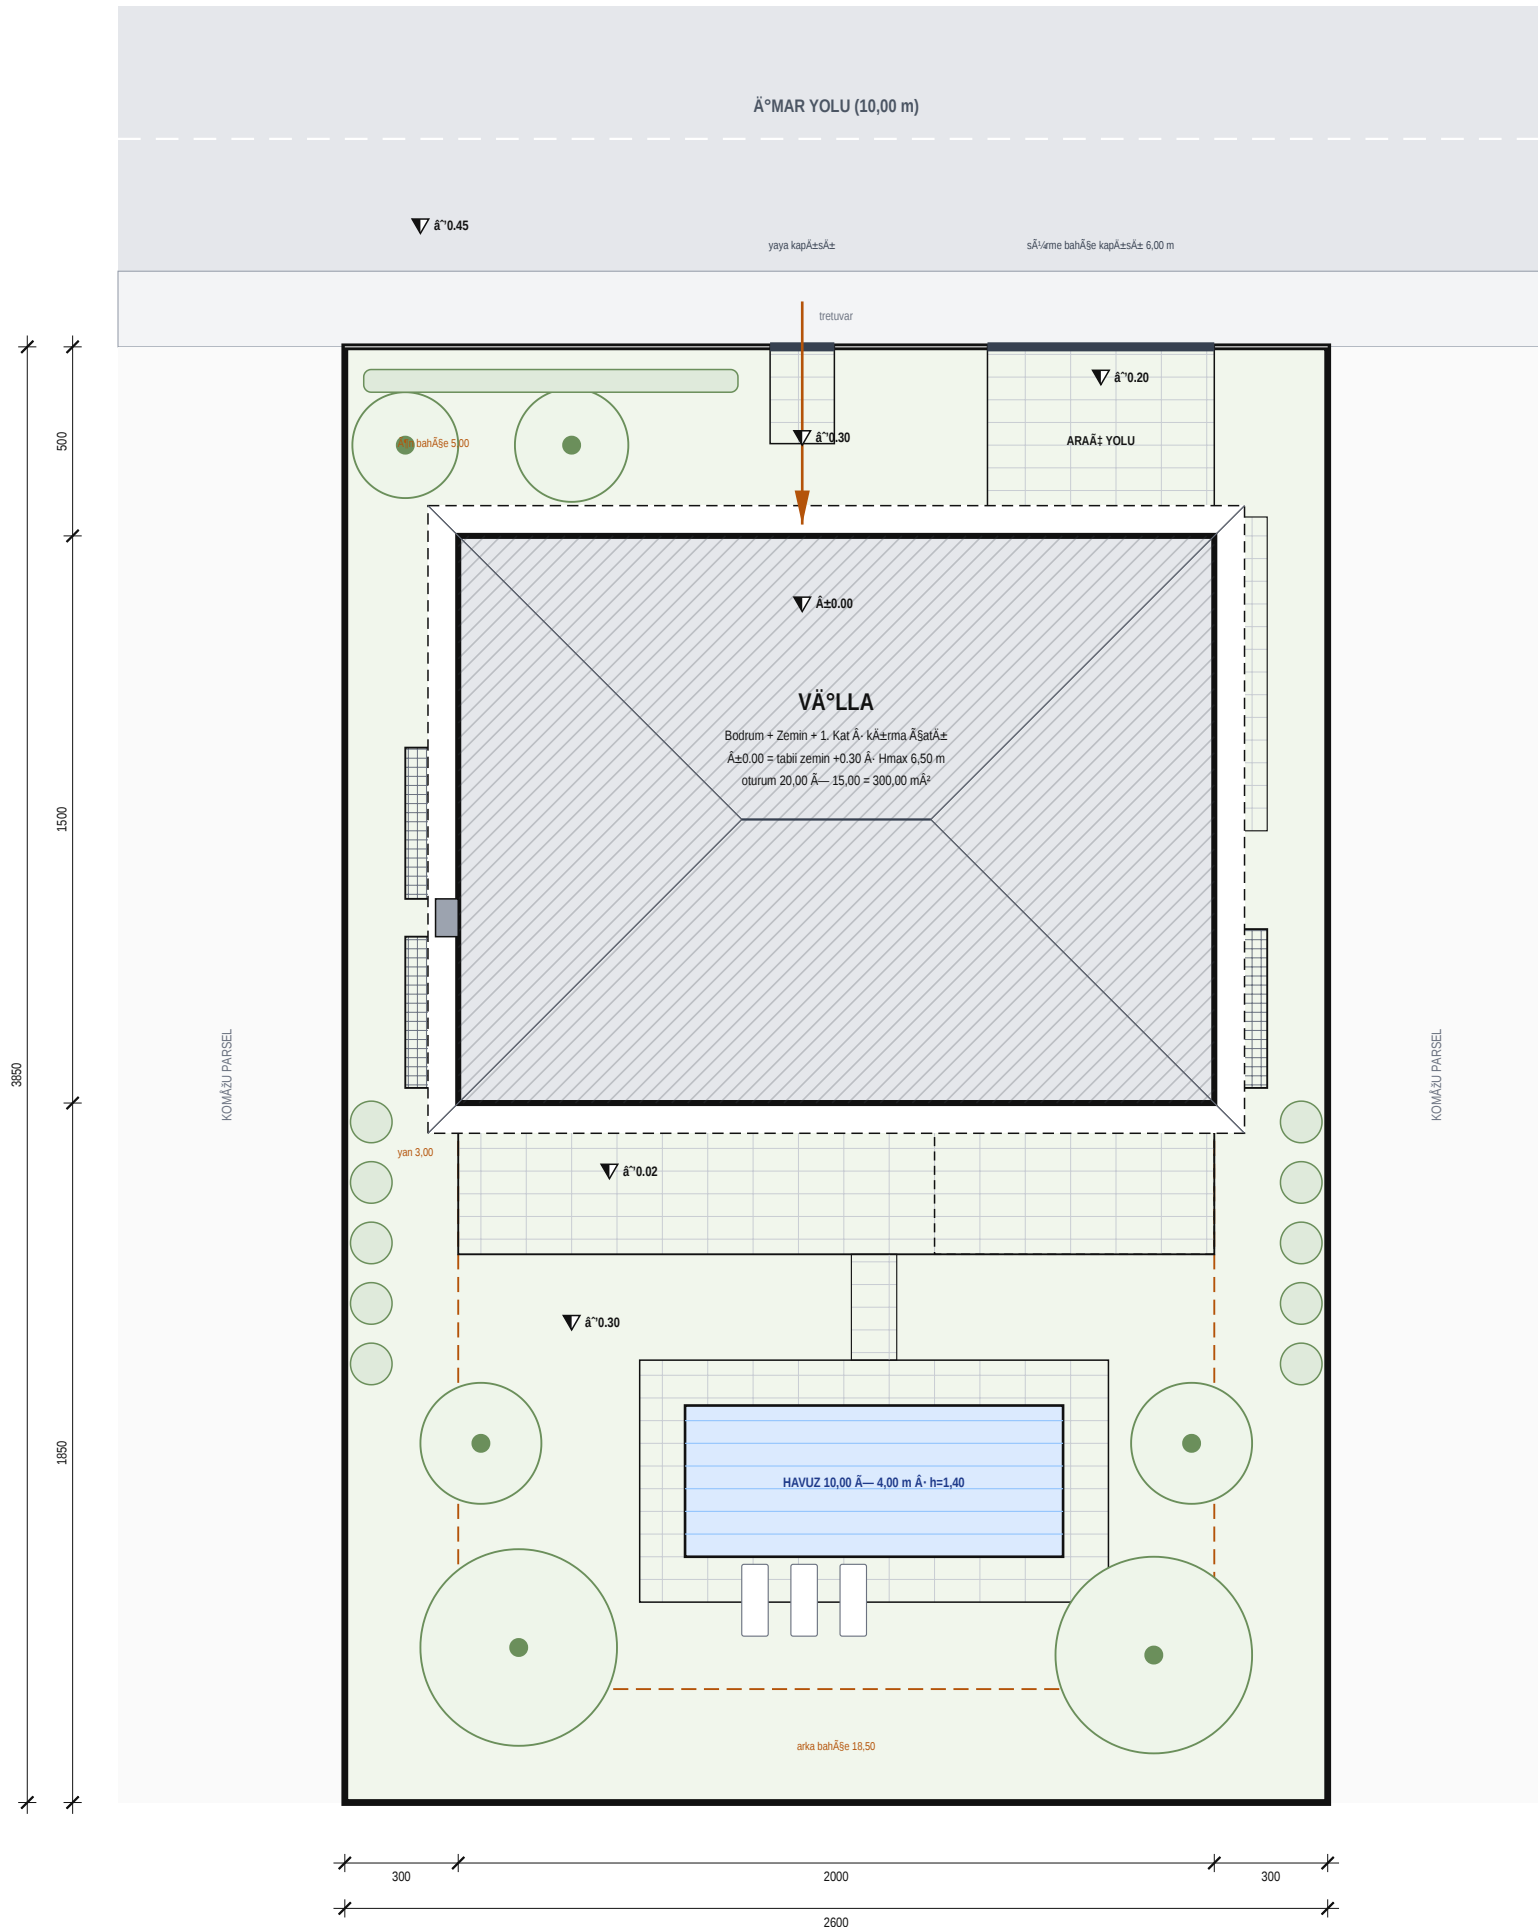

VAZÄ°YET PLANI Ä° Ä°-: 1/200

Parsel 26,00 Ä° - 38,50 = 1.001 mâ² Ä° Ä°n bahÄ°e 5,00 Ä° yan bahÄ°eler 3,00 Ä° arka bahÄ°e 18,50

Konya Â Meram Â Durunday
Bodrumlu dubleks m²1/4stakil konut Â 300 m² oturum

Ruhsat ve uygulamaya esas deÄildir

- NOTLAR

-

R0	19.09.2026	Ä°lk yayÄ±n
R1	21.09.2026	Plan kurgusu yeniden dÄ°zenlendi; kesit, gÄ°rÄ°nÄ°Å, detay ve doÄ°rama listesi eklendi

E. Ceran

A-02



DÃ¶rme kotu ≈ 3.06 Å. Net kullanÄ±m alanÄ± 242,60 m² Å. BrÃ¼t 300,00 m²

DURUNDAY VÄ°LLA

Konya Â· Meram Â· Durunday
Bodrumlu dubleks mâ±/stakil konut Â· 300 mÂ² oturum

MÂ°MARÂ° Â-N PROJE (AVAN)

Ruhsat ve uygulamaya esas deÄYildir

LEJANT

- Betonarme kolon / perde
- Duvar (gazbeton, 25 / 13,5 cm)
- IsÂ± yalÂ±tÂ±mÂ± (taÄYÄ°nÂ±/4, 8 cm)
- Cam korkuluk h=110 cm
- Porselen / fayans kaplama
- DoÄYal taÄY (traverten)
- Tesisat ÄYatÂ±
- DÄ°Ä°Yeme kotu (m)
- Aks balonu

NOTLAR

- GiriÄY kotu Â±0.00 = tabii zemin +0.30. Garaj Â°0.17, teras Â°0.02; garajdan eve El30, kendiliÄYinden kapanan kapÂ±.
- Salonâ°yemekâ°mutfak aÄ°sÂ±k plandÂ±r; gÄ°ney cephesi kaldÂ±r-sÄ°r (lift & slide) doÄYrama ile teras ve pergola aÄ°sÂ±lÂ±r.
- Misafir sÄ°iti (oda + banyo + hol) giriÄYe yakÂ±n, aile bÄ°lÄ°mÂ±nden baÄYÂ±msÂ±zdÂ±r; Ä°st kattaki yatak 2 sÄ°itiyle aynÂ± akstadÂ±r (Ä°slak hacimler Ä°st Ä°ste).
- Servis giriÄYi doÄYu yan bahÄ°sedir; araÄ° yolu â° servis kapÂ±sÂ± â° arka mutfak / kiler. Market alÂ±ÄYveriÄYi salondan geÄ°meden mutfaÄYa ulaÄYÂ±r.
- Ä°Ä°mine bacasÂ± batÂ± cephede dÄ°ÄYa taÄYan taÄY kaplÂ± kÄ°ledir; Ä°satÂ±dan 1,00 m yÄ°ksetilir.

REVÄ°ZYONLAR

R0	19.09.2026	Ä°ik yayÄ±n
R1	21.09.2026	Plan kurgusu yeniden dÄ°zenlendi; kesit, gÄ°rÄ°nÄ°ÄY, detay ve doÄYrama listesi eklendi

Ä°Ä° SAHÄ°BÄ°

â°

HAZIRLAYAN

E. Ceran

MÂ°ELLÄ°F MÂ°MAR

(ruhsat aÄYamasÂ±nda atanacak)

Ä°MZA

PAFTAADI

ZEMÄ°N KAT PLANI

Ä°LÄ°EK

1/100

TARÄ°H

21.09.2026

PAFTA NO

A-03

ZEMÄ°N KAT PLANI Â· Ä°-: 1/100

DÄ°Ä°Yeme kotu Â±0.00 Â· Net kullanÂ±m alanÂ± 246,30 mÂ² Â· BrÄ°t 300,00 mÂ²



Konya Â Meram Â Durunday
Bodrumlu dubleks m²1/4stakil konut Â 300 m² oturum

Ruhsat ve uygulamaya esas deÄildir

- ## NOTLAR
1. Ebeveyn $\bar{S}\bar{A}i\bar{A}ti$: hol $\bar{a}t\bar{a}'$ gijnime oda $\bar{S}\bar{A}t\bar{a}'$ yatak oda $\bar{S}\bar{A}t\bar{a}'$ ve banyo. Yatak oda $\bar{S}\bar{A}t\bar{a}'$ na $\bar{A}t\bar{a}'$ na tamam $\bar{A}t\bar{a}'$ hol/gijnime $\bar{A}i\bar{A}$ zzerinden girilir, her birinin kendi banyosu vard $\bar{A}t\bar{a}'$.
 2. Balkonlar 1,50 m konsoldur ($\bar{A}\bar{S}\bar{A}t\bar{a}'k\bar{a}' \bar{S}\bar{A}t\bar{a}'kma$); $\bar{A}t\bar{a}'\bar{S}\bar{A}t\bar{a}'$ $k\bar{A}'\bar{P}\bar{r}\bar{A}'i\bar{S}\bar{A}'\bar{A}$ kesici (Sch $\bar{A}'t\bar{A}'k$ Isokort) ile da $\bar{P}\bar{A}'i$ Yeme $\bar{y}e$ ba $\bar{A}$ Ylan $\bar{A}t\bar{a}'$.
 3. Giri $\bar{A}'i$ galerisi zemin katt $\bar{a}'$ 1. kat tavan $\bar{A}i\bar{A}$ na kadar $\bar{A}i\bar{S}it$ y $\bar{A}'i$ $\bar{A}$ kkelikler, kuzey cephe tam boy sobit cam.
 4. $\bar{A}t\bar{a}'\bar{A}t\bar{a}'$ ara $\bar{S}\bar{A}t\bar{a}'$ na kioridordaki katlan $\bar{A}'a$ merdivenli kapaktan $\bar{A}\bar{S}\bar{A}t\bar{a}'k\bar{A}t\bar{a}'\bar{A}t\bar{a}'$ ($y\bar{A}'i\bar{A}t\bar{a}'\bar{A}t\bar{a}'\bar{A}t\bar{a}'$, 70 $\bar{A}$ —120).
 5. Pencere denizlikleri $\bar{A}\bar{S}\bar{A}'k$ 90 cm; kap $\bar{A}'a$ boyu camlar yaln $\bar{A}'i$ $\bar{A}$ zca balkonlara $\bar{A}t\bar{a}'\bar{A}t\bar{a}'\bar{A}t\bar{a}'$.

R0	19.09.2026	Ä°lk yayÄ±n
R1	21.09.2026	Plan kurgusu yeniden dÄ°zenlendi; kesit, gÄ°rÄ°nÄ°Å, detay ve doÄ°rama listesi eklendi

HAZIRLAYAN
E. Ceran

Ä°MZA

PAFTA NO
A-04



DURUNDAY VÄ°LLA

Konya Â· Meram Â· Durunday

Bodrumlu dubleks mâ°/stakil konut Â· 300 mâ² oturum

MÂ°MARÂ° Â-N PROJE (AVAN)

Ruhsat ve uygulamaya esas deÄYildir

LEJANT

- Kil kiremit
Baca (taÄY kaplÄ±)

NOTLAR

- Â±atÄ± konstrÄ°ksiyonu ahÄYaptÄ±; betonarme Â±atÄ± dÄ°ÄYemesi Â°zerinde 14 cm taÄYÄ°nÄ° Â±sÄ± yalÄ±tÄ±mÄ± vardÄ±.
- Oluk ve yaÄYmur iniÄYleri antrasit alÄ°minyum; iniÄYler bahÄ±se drenajÄ±na ve yaÄYmur suyu deposuna baÄYlanÄ±.
- Â±atÄ± arasÄ± havalandÄ±rÄ±Ä± (saÄ±sak altÄ± menfez + mahya havalandÄ±rmasÄ±).
- GiriÄY saÄ±saÄYÄ± ekstansif yeÄYil Â±atÄ±dÄ±; pergola biyoklimatik (aÄ±Ä±Ä±r lamelli) alÄ°minyumdur.



REVÄ°ZYONLAR

R0	19.09.2026	Ä°lk yayÄ±n
R1	21.09.2026	Plan kurgusu yeniden dÄ°zenlendi; kesit, gÄ°rÄ°nÄ°ÄY, detay ve doÄYrama listesi eklendi

Ä°Ä± SAHÄ°BÄ°

â€

HAZIRLAYAN

E. Ceran

MÂ°ELLÄ°F MÂ°MAR

(ruhsat aÄYamasÄ±nda atanacak)

Ä°MZA

PAFTAADI

Ä±ATI PLANI

Ä-LÄ°EK

1/100

TARÄ°H


21.09.2026

PAFTA NO

A-05

Ä±ATI PLANI Â· Ä°: 1/100

KÄ±rma Â±atÄ± %30 Â· saÄ±sak 80 cm Â· mahya +8.94

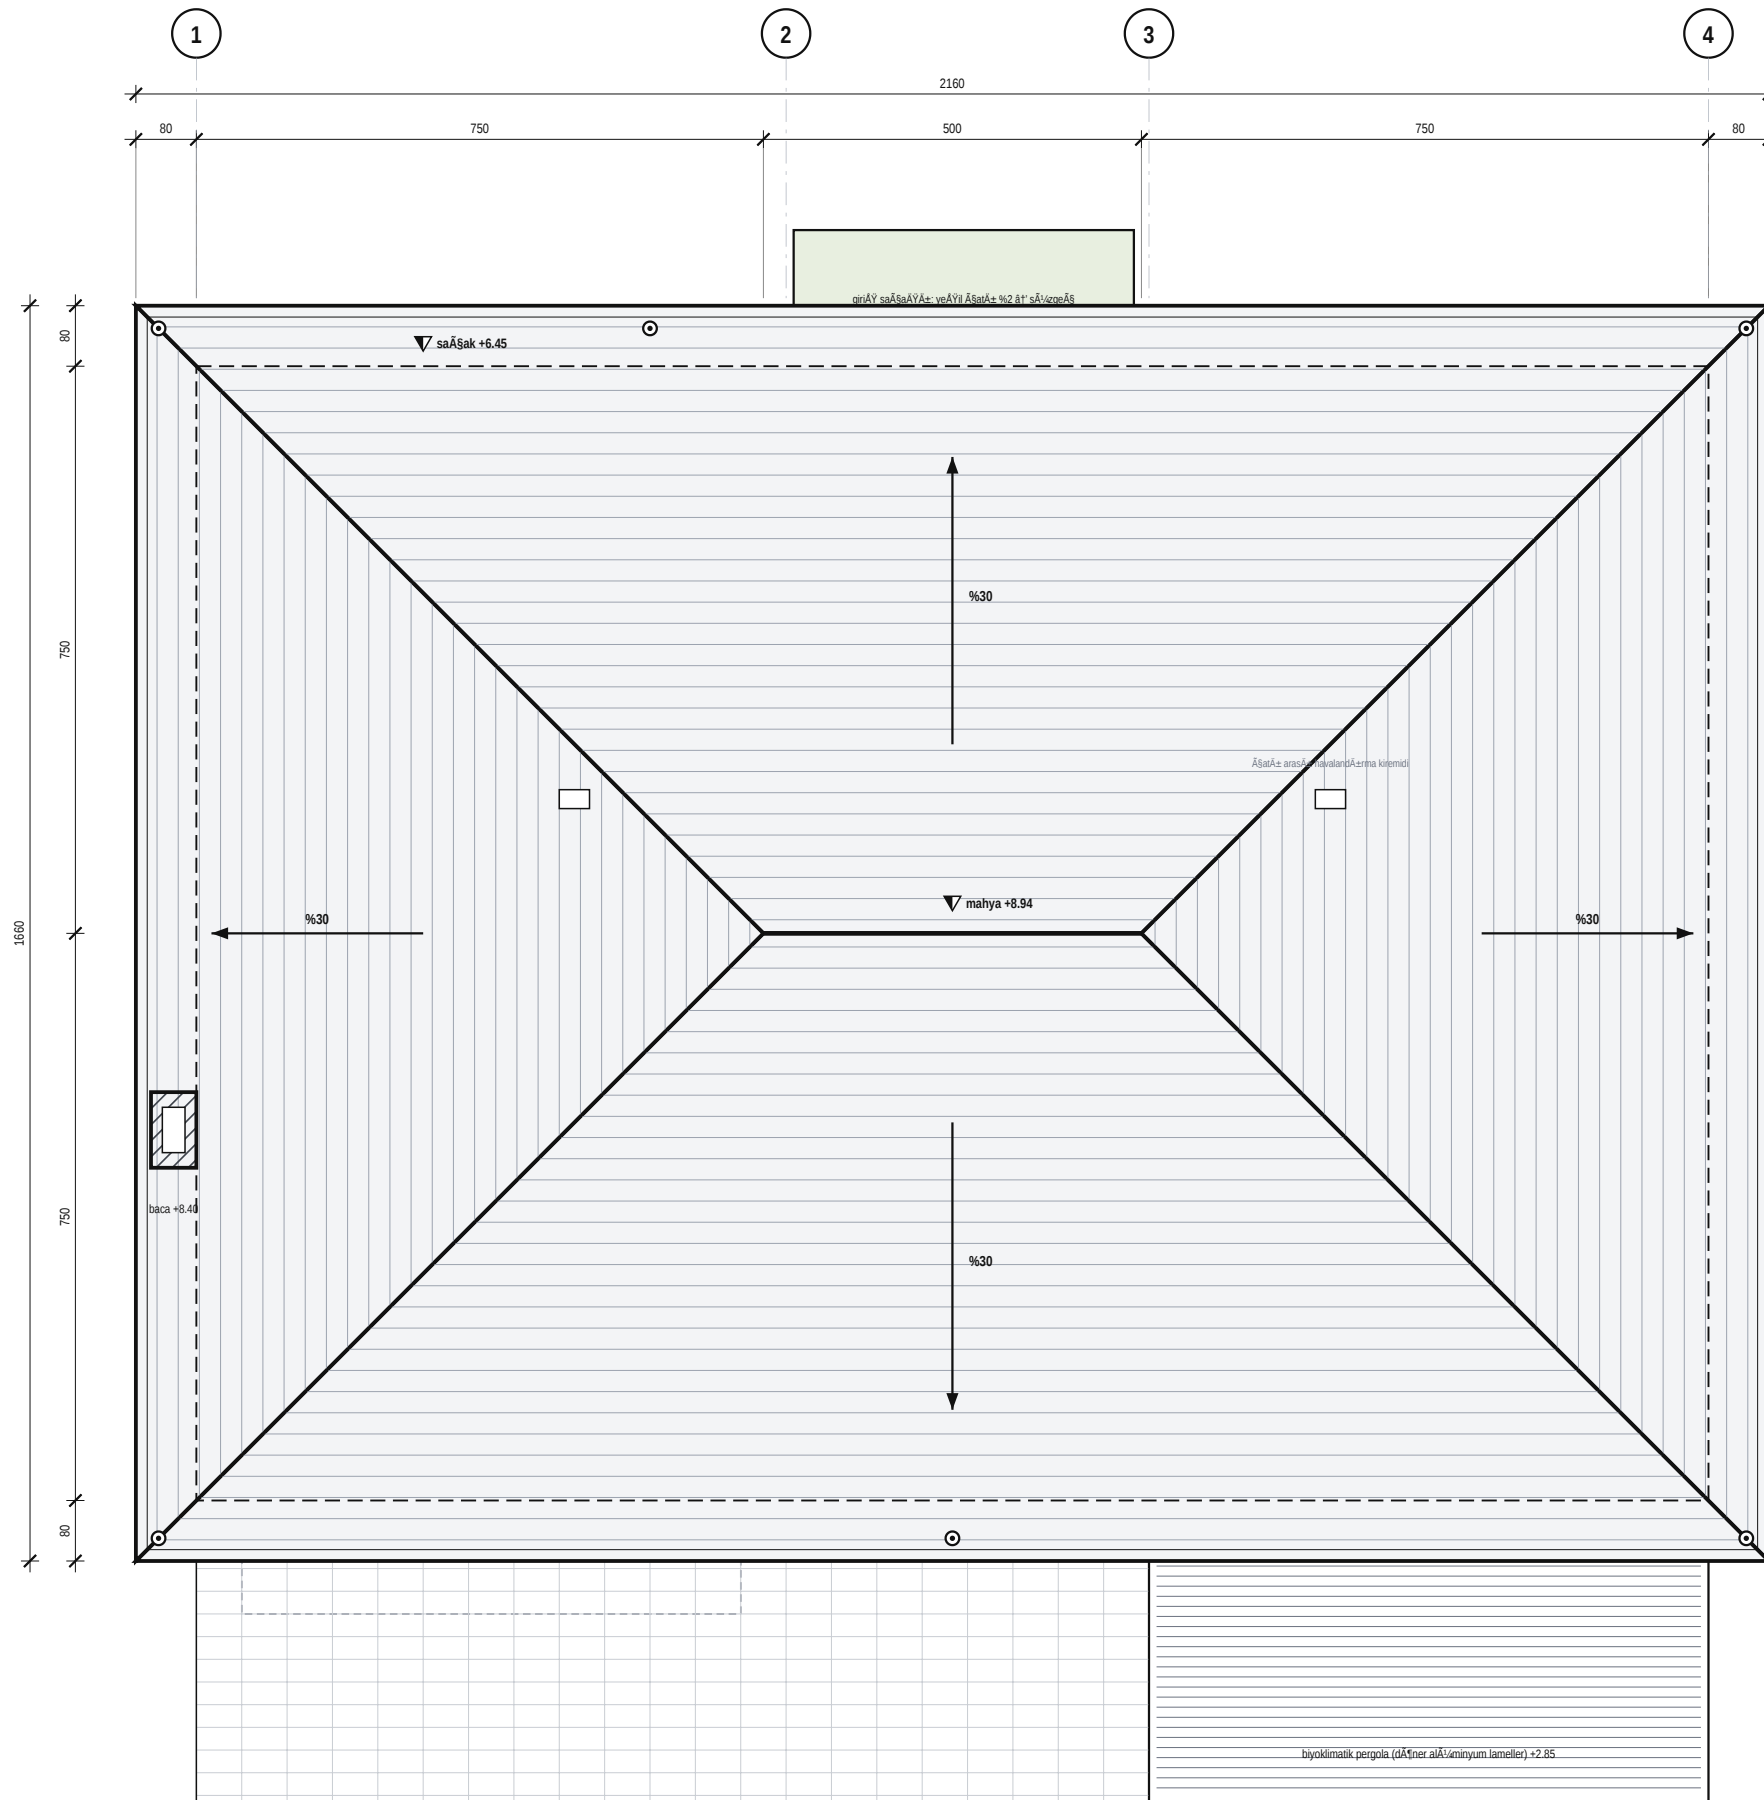

DURUNDAY VÄ°LLA

Konya Â· Meram Â· Durunday

Bodrumlu dubleks mâ°stakil konut Â· 300 mâ² oturum

MÂ°MARÂ° Â-N PROJE (AVAN)

Ruhsat ve uygulamaya esas deÄYildir

LEJANT

- Betonarme (kesilen)
▨ Duvar (kesilen)
▩ IsÂ± / su yalÂ±mÂ±
/ / DoÄYal zemin
■ Cam / doÄYrama
▼ Kot (m)

NOTLAR

- Kesit giriÄY kapÂ±sÂ±, galeri, hol ve yemek alanÂ±ndan geÄŒer; merdiven kesitin arkasÂ±nda gÂŒtrÂ±nÂ±/ÄYtedir.
- Galeri: giriÄY holÂ±/4 zemin kattan ÂŒsatÂ± dÂŒÄYemesine kadar ÂŒŒit yÂ±/4kseklidir (6,20 m).
- Kat yÂ±/4kseklileri: bodrum 3,06 Â· zemin 3,20 Â· 1. kat 3,00 m; dÂŒÄYeme 30 cm (20 plak + 10 ÂŒapıkaplama).
- Radye temel 60 cm; zemin etÂ±/dÂ±/ne gÂŒfre statik projede kesinleÄYecektir.



REVÂ°ZYONLAR

- | | | |
|----|------------|--|
| R0 | 19.09.2026 | Â°ik yayÂ±n |
| R1 | 21.09.2026 | Plan kurgusu yeniden dÂ±/zenlendi; kesit, gÂŒtrÂ±nÂ±/ÄY, detay ve doÄYrama listesi eklendi |

Â°ÂŒ SAHÂ°BÂ°

â€™

HAZIRLAYAN

E. Ceran

MÂ°CELLÂ°F MÂ°MAR

(ruhsat aÄYamasÂ±nda atanacak)

Â°MZA

PAFTAADI

Aâ€™A KESÂ°TÂ° Â· Â-: 1/100

Â-LÂ±EK


1/100

TARÂ°H

21.09.2026

PAFTA NO

A-06

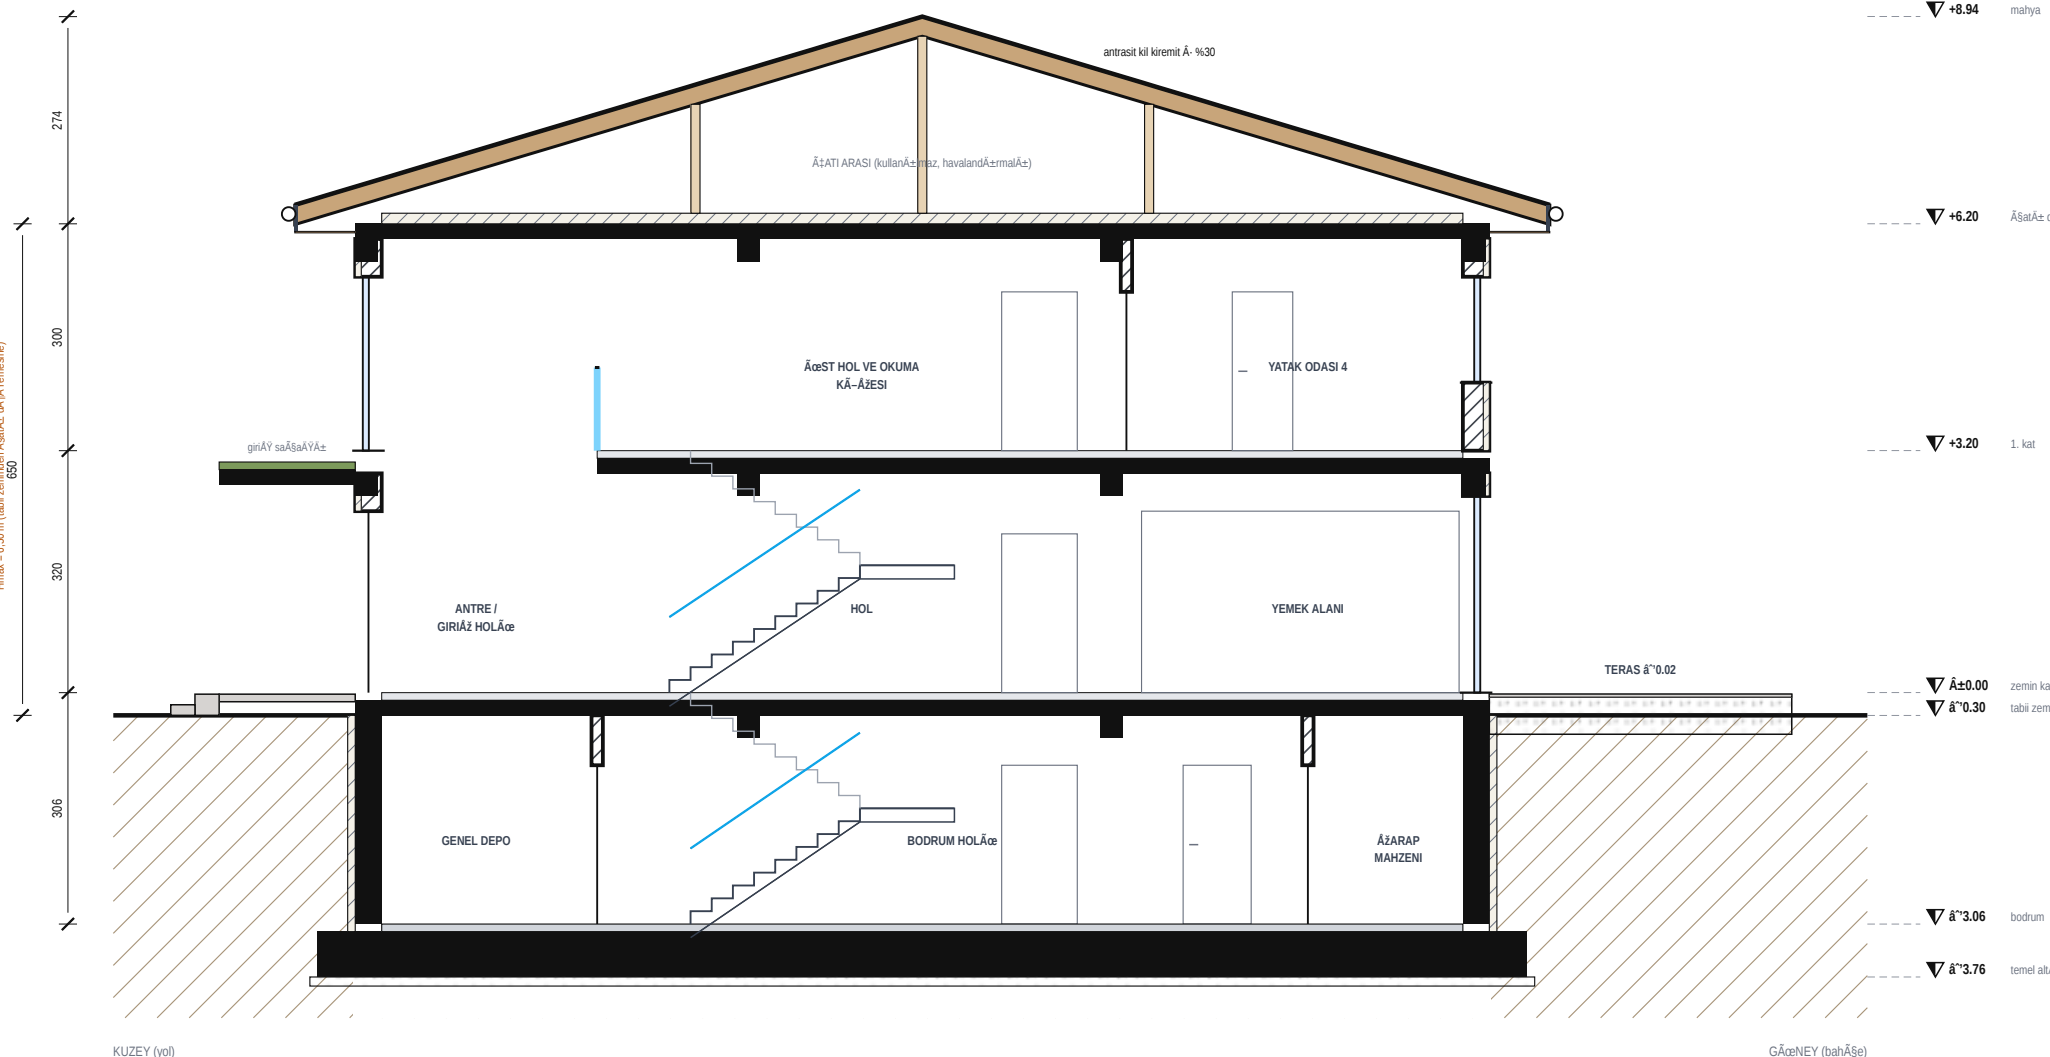

Aâ€™A KESÂ°TÂ° Â· Â-: 1/100

Kesit x = 9,20 m, doÄYuya bakÂ±ÄY (hol, galeri, yemek alanÂ±)

DURUNDAY VÄ°LLA

Konya Â· Meram Â· Durunday

Bodrumlu dubleks mâ¼stakil konut Â· 300 mâ² oturum

MÂ°MARÂ° Â-N PROJE (AVAN)


Ruhsat ve uygulamaya esas deÄYildir

LEJANT

- Betonarme (kesilen)
▨ Duvar (kesilen)
▩ IsÂ± / su yalÂ±Â±mÂ±
▧ DoÄYal zemin
■ Cam / doÄYrama
▼ Kot (m)

NOTLAR

- Kesit salonâ°yemekâ°mutfak aÂ§Â±k planÂ±ndan geÂ§er; bodrumda batÂ± ve doÄYü Â±ÄYÂ±klÂ±klarÂ± gÂ¶rÂ±lir.
- İÄYÂ±klÂ±k tabanÂ± â°3.16, sÂ±zgeÂ§li; Â±sî¼ galvaniz Â±zgara ve cam korkuluk.
- Â±mine bacasÂ± batÂ± cephede, Â±dan yÂ±kselir (+8.40).

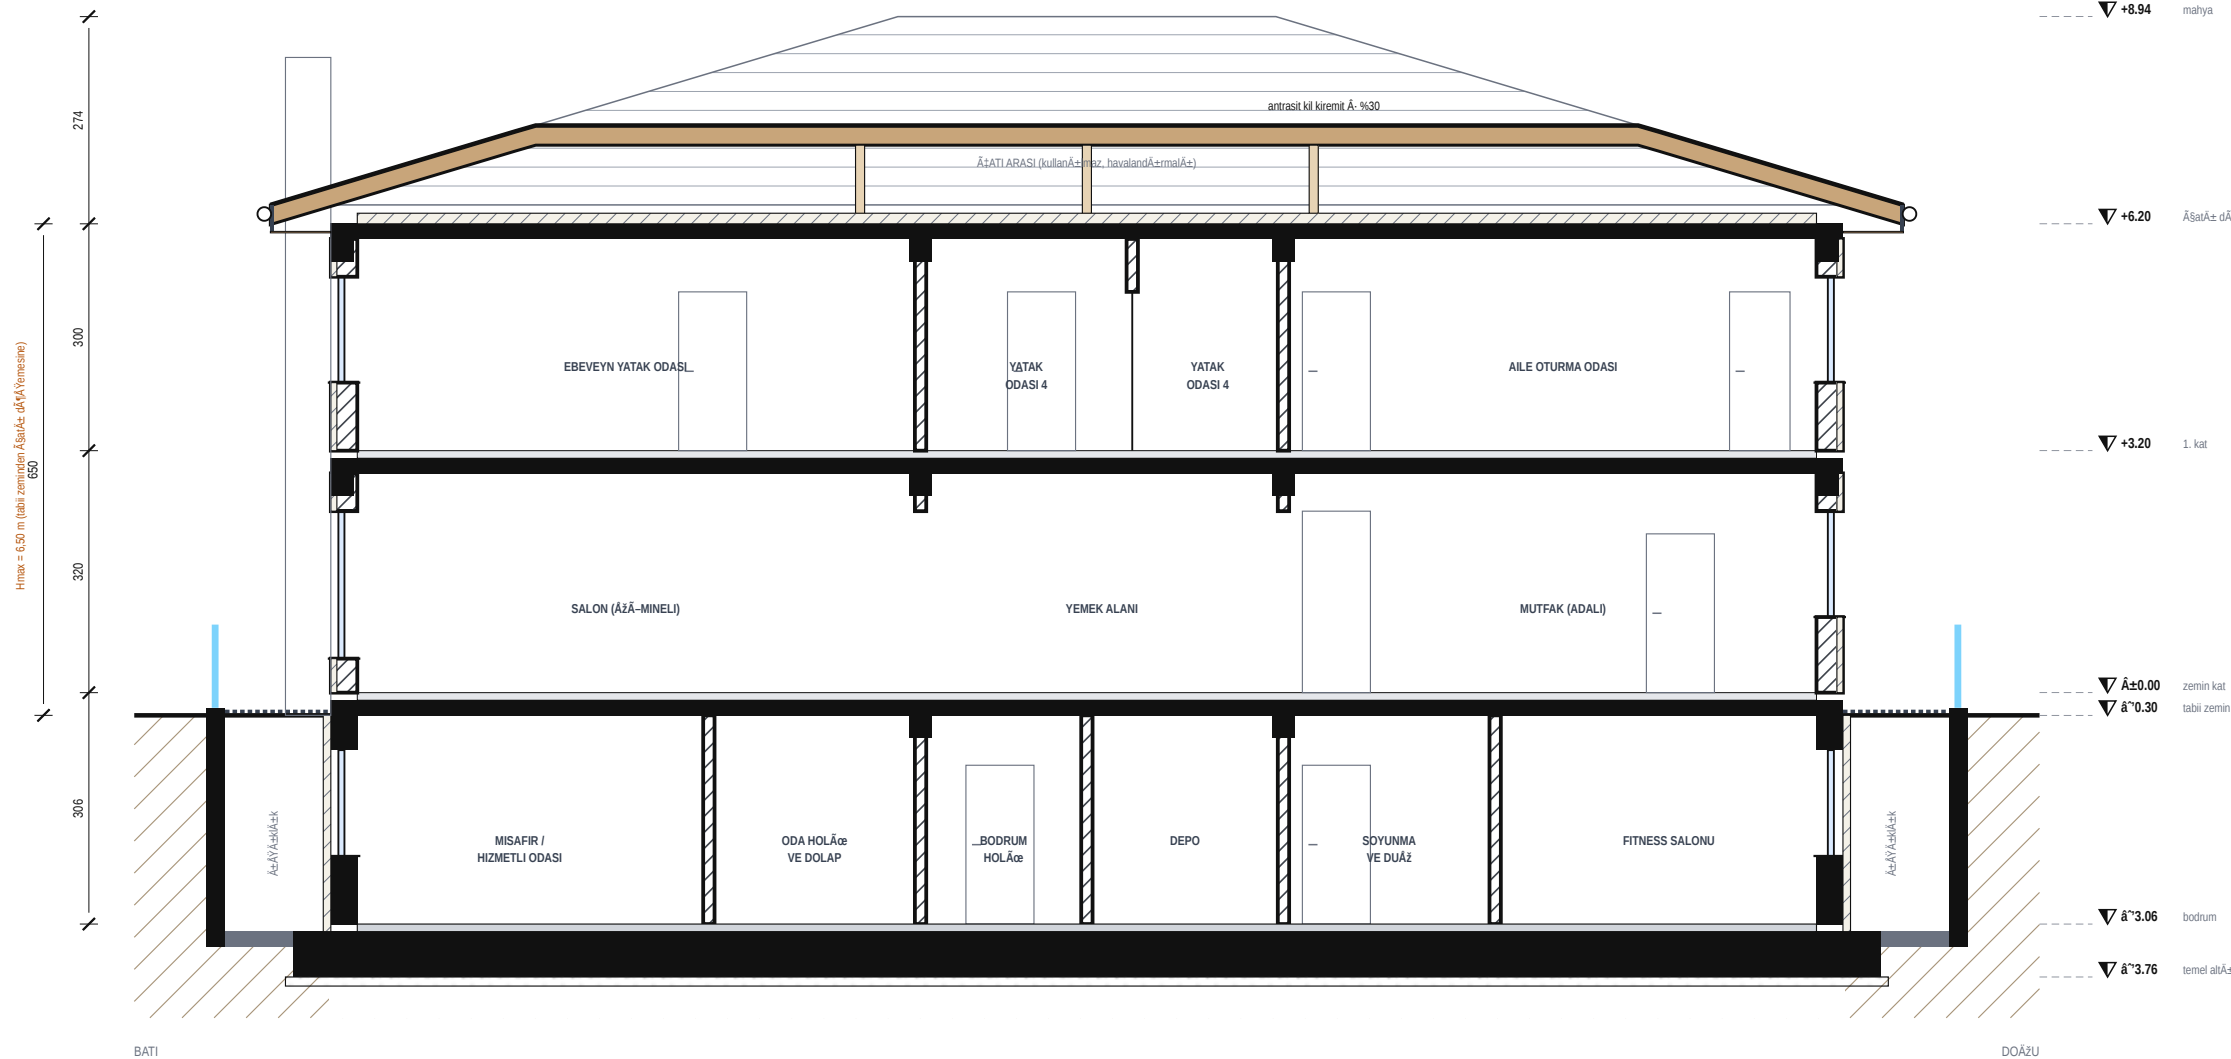

REVÂ°ZYONLAR

- R0 19.09.2026 Â°lk yayÂ±n
- R1 21.09.2026 Plan kurgusu yeniden dÂ±zenlendi; kesit, gÂ¶rÂ±lir/Â±nÂ±ÄY, detay ve doÄYrama listesi eklendi

Â°Â± SAHÂ°BÂ°

â°

HAZIRLAYAN

E. Ceran

MÂ°ELLÂ°F MÂ°MAR

(ruhsat aÄYamasÂ±nda atanacak)

Â°MZA

PAFTAADI

Bâ°B KESÂ°TÂ° Â- Â-: 1/100

Bâ°B KESÂ°TÂ° Â- Â-: 1/100

Kesit y = 12,30 m, kuzeye bakÂ±ÄY (salonâ°yemekâ°mutfak; Â±ÄYÂ±klÂ±klar)

DURUNDAY VÄ°LLA

Konya Â· Meram Â· Durunday

Bodrumlu dubleks mâ°/stakil konut Â· 300 mâ² oturum

MÂ°MARÄ° Â-N PROJE (AVAN)

Ruhsat ve uygulamaya esas deÄYildir


LEJANT

- DoÄYal taÄY kaplama (Sille taÄYÄ±)
Ä°nce silikon sÄ±va (8 cm taÄYyÄ°n/4 mantolama)
AhÄYap kompozit kaplama
Antrasit kil kiremit
IsÄ±cam, antrasit doÄYrama

NOTLAR

1. DoÄYramalar antrasit (RAL 7016) Ä±sÄ± yalÄ±mlÄ± alÄ±minyum.
2. Yatak odalarÄ±nda motorlu dÄ±ÄY jaluzy kutusu cephe iÄ±ine gÄ°mÄ°/dÄ±/dÄ±/4.
3. GÄ°aney cephesi: konsol balkonlar ve teras pergolasÄ± yazÄ±n gÄ°/neÄY kontrolÄ±/4 saÄYlar.

KUZEY GÄ-RÄ°NÄ°Ä±Ä± (GÄ°RÄ°Ä± CEPHESÄ°) Â· Ä-: 1/100

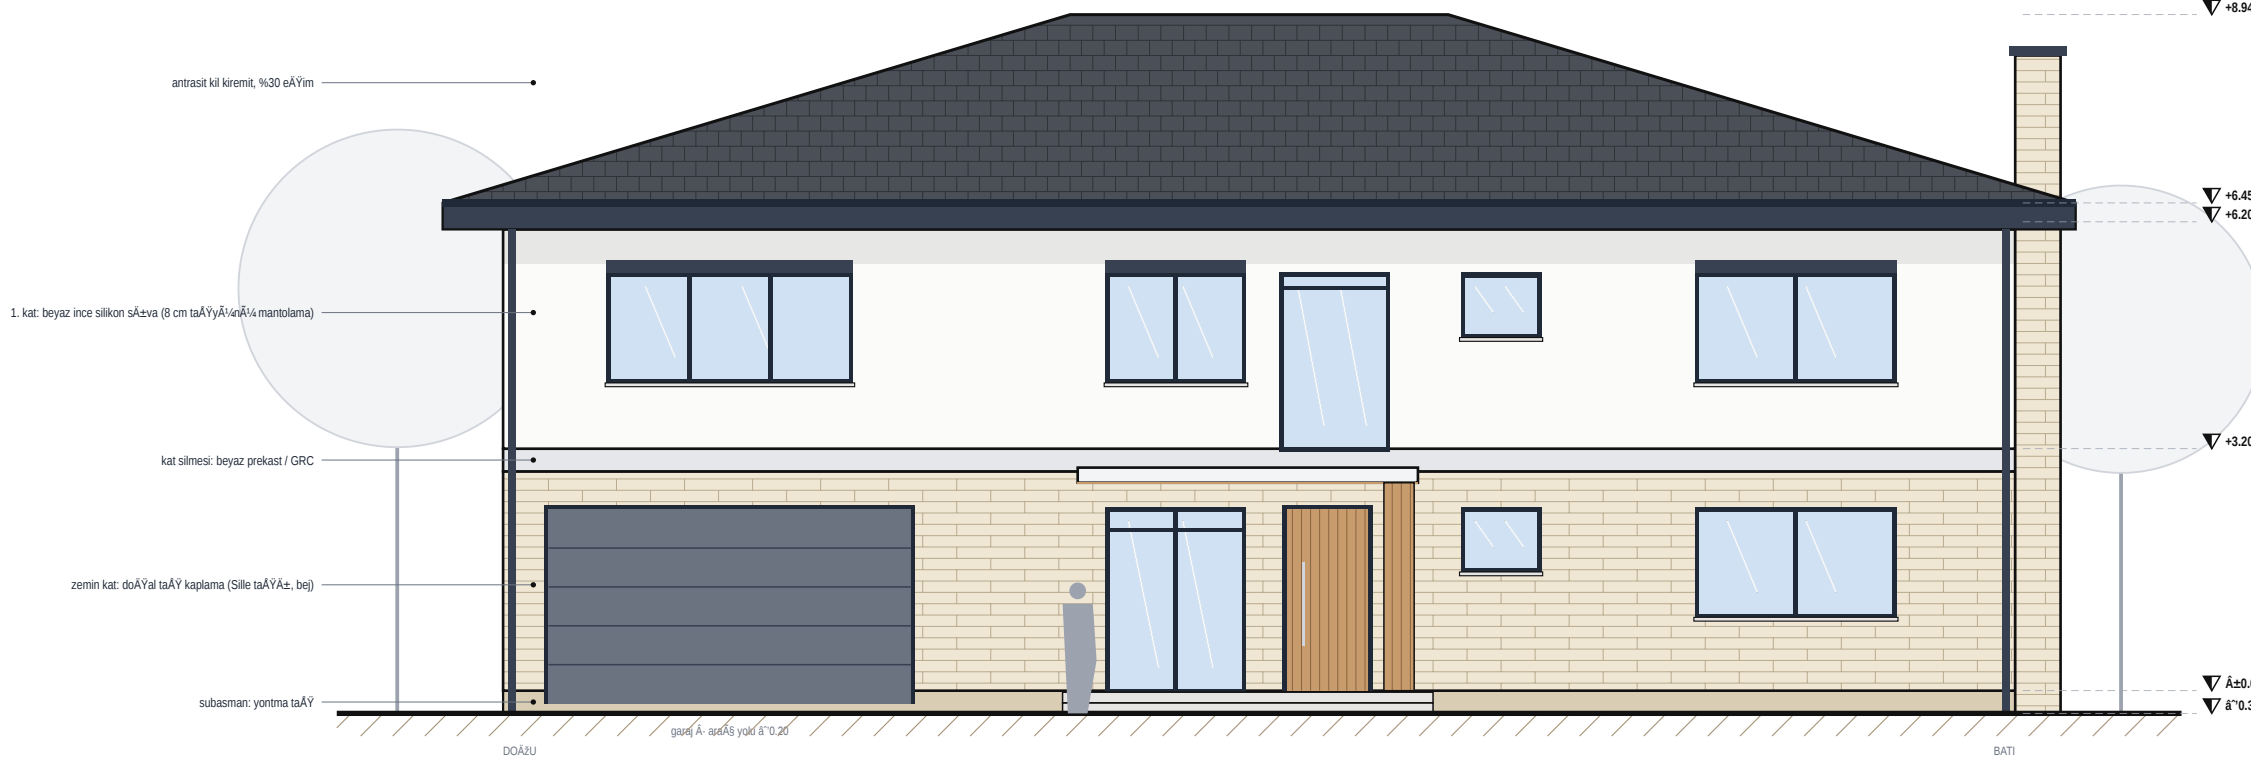

GÄ°NEY GÄ-RÄ°NÄ°Ä±Ä± (BAHÄ±E CEPHESÄ°) Â· Ä-: 1/100



REVÄ°ZYONLAR

R0	19.09.2026	Ä°lk yayÄ±n
R1	21.09.2026	Plan kurgusu yeniden dÄ±zenlendi; kesit, gÄ°/Ä±/Ä±/Ä±/Ä±, detay ve doÄYrama listesi eklendi

Ä°Ä± SAHÄ°BÄ°	HAZIRLAYAN
Ä°	E. Ceran

MÄ°ELLÄ°F MÄ°MAR	Ä°MZA
(ruhsat aÄYamasÄ±nda atanacak)	

PAFTA ADI

KUZEY VE GÄ°NEY GÄ-RÄ°NÄ°Ä±Ä±LERÄ°

Ä-LÄ±EK	TARÄ°H	PAFTA NO
1/100	21.09.2026	A-08

DURUNDAY VÄ°LLA

Konya Â· Meram Â· Durunday

Bodrumlu dubleks mâ°/stakil konut Â· 300 mâ² oturum

MÂ°MARÄ° Â-N PROJE (AVAN)

Ruhsat ve uygulamaya esas deÄYildir

LEJANT

- DoÄYal taÄY kaplama (Sille taÄYÄ±)
Ä°nce silikon sÄ±va (mantolama)
AhÄYap kompozit kaplama
Antrasit kil kiremit
IsÄ±cam, antrasit doÄYrama

NOTLAR

1. BatÄ± cephesinde ÄYÄmine bacasÄ± taÄY kaplÄ± dikey kÄ±/de olarak okunur.
2. IÄYÄ±kÄ± korkuluklarÄ± Ä±erÄ±sesiz cam, h = 110 cm.



REVÄ°ZYONLAR

R0	19.09.2026	Ä°lk yayÄ±n
R1	21.09.2026	Plan kurgusu yeniden dÄ±zenlendi; kesit, gÄ±rÄ±nÄ±ÄY, detay ve doÄYrama listesi eklendi

Ä°Ä SAHÄ°BÄ° â€™	HAZIRLAYAN E. Ceran
---------------------	------------------------

MÄ°ELLÄ°F MÄ°MAR (ruhsat aÄYamasÄ±nda atanacak)	Ä°MZA
--	-------

PAFTA ADI

DOÄŽU VE BATI GÄ-RÄ°NÄ°ÄŽLERÄ°

Ä-LÄ°EK 1/100	TARÄ°H 21.09.2026	PAFTA NO A-09
------------------	----------------------	------------------

DOÄŽU GÄ-RÄ°NÄ°ÄŽLERÄ° Â- Ä-: 1/100



BATI GÄ-RÄ°NÄ°ÄŽLERÄ° Â- Ä-: 1/100



DURUNDAY VÄ°LLA

Konya Â· Meram Â· Durunday

Bodrumlu dubleks mâ¼stakil konut Â· 300 mâ² oturma

MÂ°MARÂ° Â-N PROJE (AVAN)

Ruhsat ve uygulamaya esas deÄYildir

LEJANT

- Betonarme (kesilen)
▨ Duvar (kesilen)
▤ IsÂ± / su yalÂ±tÂ±mÂ±
/ / DoÄYal zemin
■ Cam / doÄYrama
▼ Kot (m)

NOTLAR

- IsÂ± yalÂ±tÂ±mÂ± TS 825'e gÂ¶re 3. bÂ¶lge (Konya) deÄYerleriyle; enerji kimlik belgesi hesabÂ±nda kesinleÄYir.
- Bodrum su yalÂ±tÂ±mÂ± radye altÂ±ndan perde Â¼stÂ¼ne kesintisiz; kÂ¶Åyelerde pah ve takviye bandÂ±.
- Balkon dÂ¶Åemesi Â±sÂ± kÂ¶prÂ¼ kesici elemanla (Isokorb) ana dÂ¶Åemeye baÄYlanÂ±r.
- DoÄYrama montajÂ±: iÂ¶ tarafta buhar kesici, dÂ±ÅY tarafta dÂ¶Åyona aÂ¶sÂ±k bant (RAL montaj).



REVÂ°ZYONLAR

R0	19.09.2026	Â¶k yayÂ±n
R1	21.09.2026	Plan kurgusu yeniden dÂ¼zenlendi; kesit, gÂ¶rÂ¼nÂ¼ÅY, detay ve doÄYrama listesi eklendi


Â°Â° SAHÂ°BÂ° â€	HAZIRLAYAN E. Ceran
---------------------	------------------------

MÂ°ELLÂ°F MÂ°MAR (ruhsat aÄYamasÂ±nda atanacak)	Â°MZA
--	-------

PAFTAADI

SÂ°STEM KESÂ°TÂ°

Â-LÂ°EK 1/50	TARÂ°H 21.09.2026	PAFTA NO A-10
-----------------	----------------------	------------------

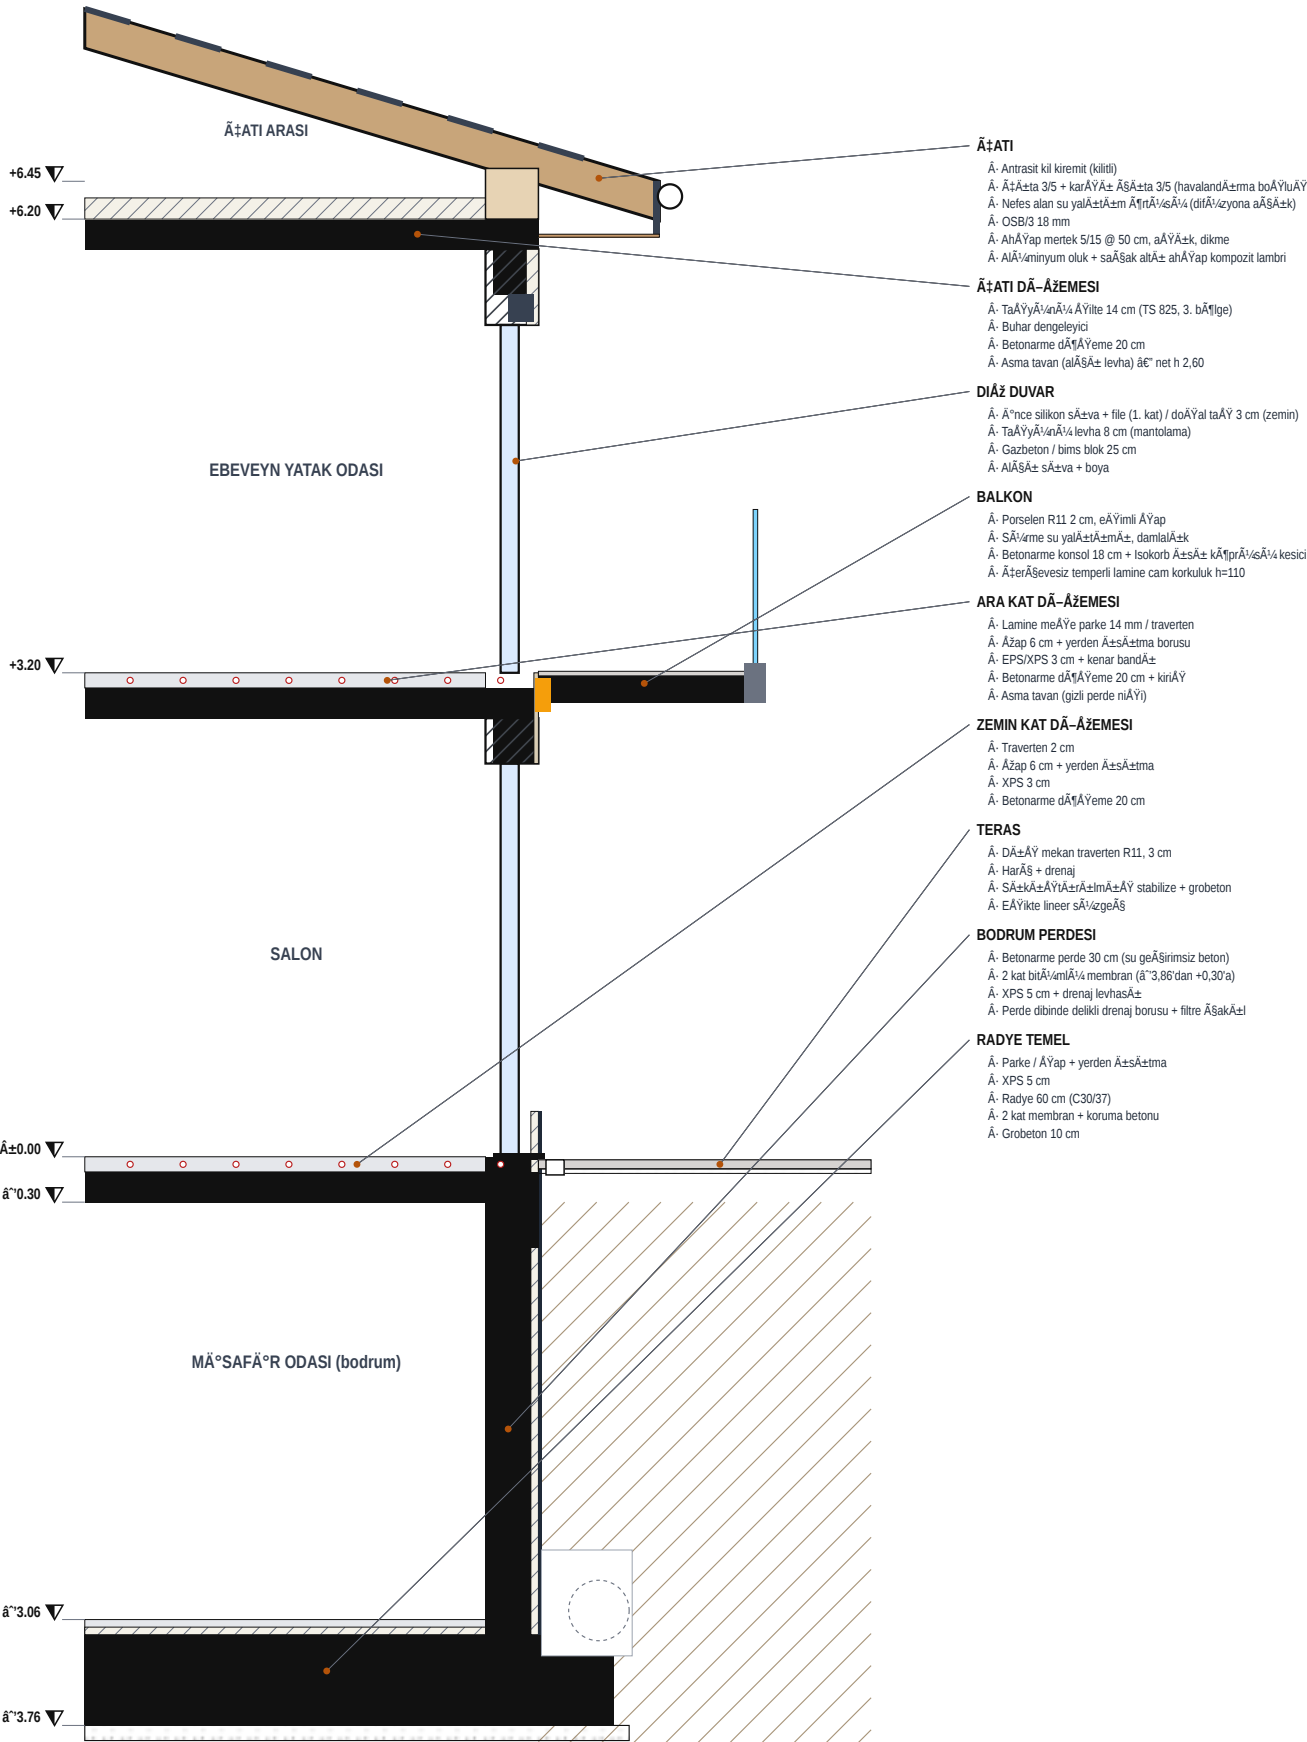

SÂ°STEM KESÂ°TÂ° SÂ°S Â· Â-: 1/50

GÂ¼ney cephesi, x = 4,00 m: bodrum misafir odasÂ± Â· salon Â· ebeveyn yatak odasÂ± ve balkon

DURUNDAY VÄ°LLA

Konya Â· Meram Â· Durunday

Bodrumlu dubleks mÂ±/stakil konut Â· 300 mÂ² oturma

MÂ°MARÂ° Â±N PROJE (AVAN)

Ruhsat ve uygulamaya esas deÄYildir

NOTLAR

- Merdiven kutusu tÂ±/m katlarda aynÂ± yerdedir (x 10,00â€²12,60 Â± y 3,20â€²8,00).
- Bodrumâ± zemin 18 rÂ±ht (9+9), zeminâ±1. kat 19 rÂ±ht (10+9); basamak 28 cm.



REVÂ°ZYONLAR

R0	19.09.2026	Â±lk yayÂ±n
R1	21.09.2026	Plan kurgusu yeniden dÂ±/zenlendi; kesit, gÂ±rÂ±nÂ±/Â±Y, detay ve doÄYrama listesi eklendi


Â±Â± SAHÂ±BÂ± â€²	HAZIRLAYAN E. Ceran
----------------------	------------------------

MÂ±ELLÂ±F MÂ±MAR (ruhsat aÄYamasÂ±nda atanacak)	Â±MZA
--	-------

PAFTAADI

MERDÂ°VEN DETAYI

Â±LÂ±EK 1/50	TARÂ±H 21.09.2026	PAFTA NO A-11
-----------------	----------------------	------------------

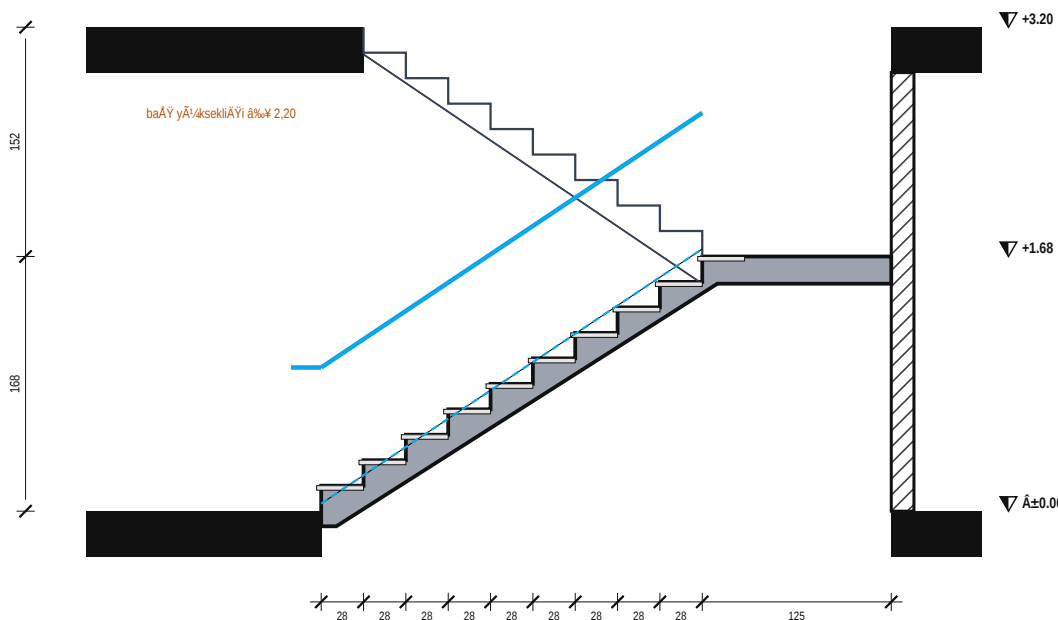

KESÂ°T Mâ€²M (batÂ± kol) Â± Â±: 1/50


MERDÂ°VEN HESABI (PAÂ°Y Md. 32 â€² konut iÂ±i merdiven)

Kat	YÂ±/kseklik	RÂ±ht	Basamak	2r + b	Kol / sahanlÂ±k
Bodrum â± Zemin	3,06 m	18 Â± 17,0 cm	28 cm	62,0	1,20 / 1,25 m
Zemin â± 1. Kat	3,20 m	19 Â± 16,8 cm	28 cm	61,7	1,20 / 1,25 m
SÂ±nÂ±r deÄYer	â€²	â€² 17,5 cm	â€² 26 cm	60â€²64	â€² 1,00 m

Â± Basamak ve sahanlÂ±k: 3 cm traverten, 2 cm rÂ±ht; basamak burnunda kaymaz kanal.
Â± Korkuluk: 10+10 mm temperli lamine cam, zemine gÂ±rime alÂ±/inyum U profil, h = 100 cm (basamak burnundan), paslanmaz kÂ±/peÂ±te Â±42.
Â± Duvar taratÂ±nda Â±40 paslanmaz kÂ±/peÂ±te h = 90 cm; LED basamak aydÂ±nlatmasÂ± (her 3 basamakta bir).
Â± Kol altÂ±: betonarme plak 18 cm, alttan alÂ±sÂ± sÂ±va + boya; sahanlÂ±k asansÂ±r perdesine oturur.

MERDÂ°VEN DETAYI Â± Â±: 1/50

Â±ki kollu (U) merdiven, betonarme, traverten kaplama, cam korkuluk

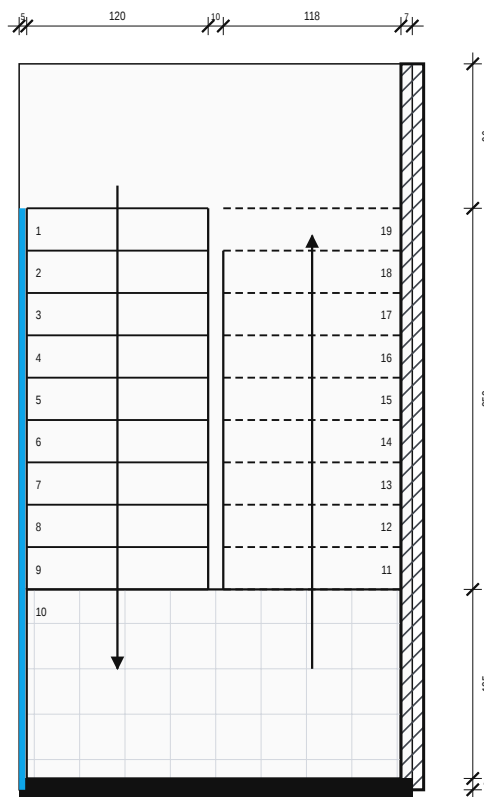

PLAN (zemin kat) Â± Â±: 1/50

P11

1 adet

Yâvâksek pencere (buzlu) 240 110

denizlik 120 1K B

P12 **5 adet**

YÃ¼ksek pencere (buzlu) 100 Å— 80

denizlik 150/160 Å— 1K D, 1K K, Z D, Z K

P13

3 adet

İAŸÄ±kİÄ±k penceresi Â· 340 Â— 140

denizlik 90 Â· B B, B D

P09

1 adet

Sabit cam 180 240

denizlik 0 2 K

P10 **1 adet**

A diagram showing a light blue rectangular block with a black outline, positioned on a dashed horizontal line. The block is centered horizontally within the diagram area.

Sabit cam $\hat{A}$ 140 Å— 230
denizlik 0 Å- 1K K

1. $\bar{A} - \bar{I}\bar{A}\bar{S}\bar{A} / \text{ler kaba in}\bar{A}\bar{Y}\text{aat bo}\bar{A}\bar{Y}\text{lu}\bar{A}\bar{Y}\text{udur (cm); imalat } \bar{A}\bar{I}\text{ncesi yerinde al}\bar{A}\bar{n}\text{acakt}\bar{A}\bar{r}.$
2. $\bar{T}\bar{A} / \text{m d}\bar{A}\bar{n}\bar{A}\bar{Y} \text{ do}\bar{A}\bar{Y}\text{ramalar Uw } \bar{a}\bar{m} \approx 1,4 \text{ W/m}\bar{A}^2\text{K; yatak odalar}\bar{A}\bar{n}\text{da sineklik ve motorlu jalu}.$
3. $\text{Kap}\bar{A}\bar{n} \text{ kodlar}\bar{A}\bar{n} \text{ plan paftalar}\bar{A}\bar{n}\text{daki kap}\bar{A}\bar{n} \text{ yerleriyle e}\bar{A}\bar{Y}\text{le}\bar{A}\bar{Y}\text{ir.}$

Kod	TÃ¼r	GeniYÃ¼k A— yÃ¼kseklik	Adet	Katlar	AÃ§Ã¼klama
K01	Villa giriÃ¼ kapÃ¼sÃ¼ (Ã§elik, ahÃ¼p kaplama)	110 Ã— 240	1	Zemin	Ã§elik iskelet, ahÃ¼p kompozit kaplama, akÃ¼llÃ¼ kilit, Ã¼st eÃ¼k titili
K02	Servis dÃ¼rÃ¼ kapÃ¼sÃ¼ (Ã¼sÃ¼ yalÃ¼mlÃ¼)	90 Ã— 210	1	Zemin	IsÃ¼ yalÃ¼mlÃ¼ alÃ¼minyum, antrasit, yarÃ¼m cam
K03	Seksiyonel garaj kapÃ¼sÃ¼ (motorlu)	480 Ã— 240	1	Zemin	YalÃ¼mlÃ¼ panel 42 mm, motorlu, fotosel
K04	Ã¼ft kanatÃ¼ cam panelli kapÃ¼	160 Ã— 240	2	Bodrum, Zemin	AlÃ¼minyum Ã§erÃ§eve, temperli buzlu cam panel
K05	Lake iÃ§ kapÃ¼ (kanatÃ¼)	90 Ã— 210	25	Bodrum, Zemin, 1. Kat	Amerikan panel gÃ¼vde, akrilik lake, gizli menteÃ¼e, manyetik kilit
K06	Lake iÃ§ kapÃ¼ (kanatÃ¼)	80 Ã— 210	8	Bodrum, Zemin, 1. Kat	Amerikan panel gÃ¼vde, akrilik lake, gizli menteÃ¼e, manyetik kilit
K07	YangÃ¼n kapÃ¼sÃ¼ EI30, kendiliÃ¼yinden kapanÃ¼r	90 Ã— 210	2	Bodrum, Zemin	EI30 sertifikalÃ¼ Ã§elik, kapÃ¼ kapatÃ¼cÃ¼, duman contasÃ¼
K08	Duvar iÃ§i sÃ¼rme kapÃ¼	90 Ã— 240	1	Zemin	Gizli kasalÃ¼ sÃ¼rme (Eclisse) / sauna: temperli cam
K09	Duvar iÃ§i sÃ¼rme kapÃ¼	80 Ã— 240	1	Bodrum	Gizli kasalÃ¼ sÃ¼rme (Eclisse) / sauna: temperli cam
K10	AsansÃ¼r kat kapÃ¼sÃ¼ (teleskopik)	100 Ã— 210	3	Bodrum, Zemin, 1. Kat	AsansÃ¼r firmasÃ¼ tedariki, paslanmaz
K11	Ã¼ft servis kapaÃ¼Ã¼	60 Ã— 60	3	Bodrum, Zemin, 1. Kat	MenteÃ¼eli servis kapaÃ¼Ã¼, kilitle

